


|              |           |                   |                                                    |                     |                     |                     |                |                  |         |                  |                                             |                      |
|--------------|-----------|-------------------|----------------------------------------------------|---------------------|---------------------|---------------------|----------------|------------------|---------|------------------|---------------------------------------------|----------------------|
|              |           | 1                 | 2                                                  | 3                   | 4                   | 5                   | 6              | 7                | 8       |                  |                                             |                      |
| A            | 建築概要      | 物件名               |                                                    |                     | 用途地域                | 第1種低層住居専用地域・第2種住居地域 |                |                  |         |                  |                                             |                      |
|              |           | 所在地               |                                                    |                     | 防火地域                | 指定無し                |                |                  |         |                  |                                             |                      |
|              |           | 敷地面積              | 299.21 m <sup>2</sup> (90.52坪)                     |                     | その他の地域・地区           | 10m高度地区・20m高度地区     |                |                  |         |                  |                                             |                      |
|              |           | 構造・規模             | 鉄筋コンクリート造+木造 (混構造) 2階建て                            |                     |                     | 宅地造成等規制区域           |                |                  |         |                  |                                             |                      |
|              |           | 建築面積              | 123.20 m <sup>2</sup> (37.27坪) 建蔽率 41.18%          |                     |                     |                     |                |                  |         |                  |                                             |                      |
|              |           | 延床面積              | 245.10 m <sup>2</sup> (74.14坪) 容積率 81.92%          |                     | 前面道路                | 北:6m                |                |                  |         |                  |                                             |                      |
|              |           |                   | 1階:122.55m <sup>2</sup> 2階:122.55m <sup>2</sup>    |                     | 建ぺい率                | 50%・60%             |                |                  |         |                  |                                             |                      |
| B            | 外部仕上表     | 施工床面積             | 296.7 m <sup>2</sup> (89.75坪)                      |                     | 容積率                 | 150%・200%           |                |                  |         |                  |                                             |                      |
|              |           | 屋根                | ガルバリウム鋼板t0.4 立はぜ葺 (立平葺)                            |                     | テラス・ポーチ床            | コンクリートコテ仕上げ         |                |                  |         |                  |                                             |                      |
|              |           |                   | アスファルトルーフィング (22kg/巻) +合板t12下地                     |                     | 軒天井                 | 珪酸カルシウム板t6 EP       |                |                  |         |                  |                                             |                      |
|              |           |                   | 断熱材:グラスウールt100 (10kg/m <sup>3</sup> ) <sup>2</sup> |                     | 外部幅木                | コンクリート打放し           |                |                  |         |                  |                                             |                      |
|              |           | 外壁 1              | コンクリート打放し フッ素樹脂クリヤー 耐火                             |                     | 軒樋                  | ガルバリウム鋼板t0.4        |                |                  |         |                  |                                             |                      |
|              |           | 外壁 2              | 耐水PBt12.5下地 ガルバリウム鋼板スバンドレル張                        |                     | 縦樋                  | ステンレスパイプ80φ         |                |                  |         |                  |                                             |                      |
|              |           | 告示1359号 第1-11 (2) | 断熱材:グラスウールt75 (10kg/m <sup>3</sup> ) <sup>2</sup>  |                     | 水切り類                | アルミ                 |                |                  |         |                  |                                             |                      |
| C            | 内部仕上表     | 外壁 3              | セメント系サイディングボードt12下地 ジョリパット吹付 PCO30BE-9201          |                     | 外部開口部               | アルミサッシ              |                |                  |         |                  |                                             |                      |
|              |           |                   | 断熱材:グラスウールt75 (10kg/m <sup>3</sup> ) <sup>2</sup>  |                     |                     |                     |                |                  |         |                  |                                             |                      |
|              |           | 階                 | 室 名                                                | 天井高                 | 床                   | 幅 木                 | 壁              | 天 井              | 備 考     |                  |                                             |                      |
|              |           | D                 | 1 玄関                                               | CH=2530             | モルタル                | 磁器質100角タイル          | 化粧MDF H=60     | PBt12.5          | ビニルクロス  | PBt9.5           | ビニルクロス                                      | 玄関収納                 |
|              |           |                   |                                                    | FL-100              |                     |                     |                |                  |         |                  |                                             |                      |
|              |           |                   | 廊下                                                 | CH=2430             | 合板t12               | MDFフローリングボードt6      | ↑              | ↑                | ↑       | ↑                | ↑                                           |                      |
|              |           |                   |                                                    | FL±0                | 断熱材:発泡ポリスチレンフォームt25 |                     |                |                  |         |                  |                                             |                      |
| リビングダイニング    | CH=2430   |                   | ↑                                                  | ↑                   | ↑                   | ↑                   | ↑              | ↑                | ↑       | カーテンレール          |                                             |                      |
|              | FL±0      |                   |                                                    |                     |                     |                     |                |                  |         |                  |                                             |                      |
| E            | 内部仕上表     | キッチン              | CH=2430                                            | ↑                   | ↑                   | ↑                   | 耐水PBt12.5      | ビニルクロス (QM-9416) | PBt9.5  | ビニルクロス (QM-9416) | 流し台:L=2250 レンジフード:L=600 吊戸棚:H=500,W=900+750 |                      |
|              |           |                   | FL±0                                               |                     |                     |                     |                | 一部化粧ケイカル板t6      |         |                  | 棚:木製OP                                      |                      |
|              |           | 洗面脱衣              | CH=2230                                            | 合板t12               | クッションフロアt2.0        | 軟質ビニル幅木 H=60        | 耐水PBt12.5      | ビニルクロス           | PBt9.5  | ビニルクロス           | 洗面化粧台:L=600 洗濯機パン:W=750 タオル掛:L=500          |                      |
|              |           |                   | FL±0                                               | 断熱材:発泡ポリスチレンフォームt25 |                     |                     |                |                  |         |                  | 棚:塩ビシート貼                                    |                      |
|              |           | WC                | CH=2230                                            | ↑                   | ↑                   | ↑                   | ↑              | ↑                | ↑       | ↑                | ペーパーホルダー タオル掛 棚:木製OP                        |                      |
|              |           |                   | FL±0                                               |                     |                     |                     |                |                  |         |                  |                                             |                      |
|              |           | F                 | 内部仕上表                                              | 2 廊下                | CH=2150             | 合板t12               | MDFフローリングボードt6 | 化粧MDF H=60       | PBt12.5 | ビニルクロス           | ↑                                           | ↑                    |
| FL±0         |           |                   |                                                    |                     |                     |                     |                |                  |         |                  |                                             |                      |
| 洋室 1         | CH=3300   |                   |                                                    | ↑                   | ↑                   | ↑                   | ↑              | ↑                | ↑       | ↑                | ↑                                           | カーテンレール              |
|              | FL±0      |                   |                                                    |                     |                     |                     |                |                  |         |                  |                                             |                      |
| 洋室 2         | CH=2310   |                   |                                                    | ↑                   | ↑                   | ↑                   | ↑              | ↑                | ↑       | ↑                | ↑                                           | カーテンレール              |
|              | FL±0      |                   |                                                    |                     |                     |                     |                |                  |         |                  |                                             |                      |
| ウォークインクローゼット | CH=2150   |                   |                                                    | ↑                   | ↑                   | ↑                   | ↑              | ↑                | ↑       | ↑                | ↑                                           | ハンガーパイプ 東側室のみカーテンレール |
| G            | 内部仕上表     | R ロフト             | CH=1400                                            | ↑                   | ↑                   | ↑                   | ↑              | ↑                | ↑       | ↑                |                                             |                      |
|              |           |                   | FL±0                                               |                     |                     |                     |                |                  |         |                  |                                             |                      |
|              |           | 共通 階段             |                                                    |                     | 化粧LVL               | 化粧LVL               | ↑              | ↑                | ↑       | ↑                | ↑                                           | 木製手すり                |
|              |           |                   |                                                    |                     |                     |                     |                |                  |         |                  |                                             |                      |
|              |           | 収納                |                                                    | 合板t12               | MDFフローリングボードt6      | 雑巾摺り                | PBt9.5         | ビニルクロス           | ↑       | ↑                | ↑                                           | クローゼットにはハンガーパイプ      |
|              |           |                   |                                                    |                     |                     |                     |                |                  |         |                  |                                             |                      |
|              |           |                   |                                                    |                     |                     |                     |                |                  |         |                  |                                             |                      |
| H            | 不燃・準不燃リスト |                   |                                                    |                     |                     |                     |                |                  |         |                  |                                             |                      |
|              |           | PBt12.5           | NM-8619                                            |                     |                     |                     |                |                  |         |                  |                                             |                      |
|              |           | PBt9.5            | QM-9828                                            |                     |                     |                     |                |                  |         |                  |                                             |                      |
|              |           | 耐水PBt12.5         | NM-9639                                            |                     |                     |                     |                |                  |         |                  |                                             |                      |
|              |           | 化粧ケイカル板           | NM-8579                                            |                     |                     |                     |                |                  |         |                  |                                             |                      |
|              |           |                   |                                                    |                     |                     |                     |                |                  |         |                  |                                             |                      |
|              |           |                   |                                                    |                     |                     |                     |                |                  |         |                  |                                             |                      |
|              | 1         | 2                 | 3                                                  | 4                   | 5                   | 6                   | 7              | 8                |         |                  |                                             |                      |

|   |           |           |         |  |  |  |  |  |  |  |
|---|-----------|-----------|---------|--|--|--|--|--|--|--|
|   |           |           |         |  |  |  |  |  |  |  |
| H | 不燃・準不燃リスト |           |         |  |  |  |  |  |  |  |
|   |           | PBt12.5   | NM-8619 |  |  |  |  |  |  |  |
|   |           | PBt9.5    | QM-9828 |  |  |  |  |  |  |  |
|   |           | 耐水PBt12.5 | NM-9639 |  |  |  |  |  |  |  |
|   |           | 化粧ケイカル板   | NM-8579 |  |  |  |  |  |  |  |
|   |           |           |         |  |  |  |  |  |  |  |
|   |           |           |         |  |  |  |  |  |  |  |
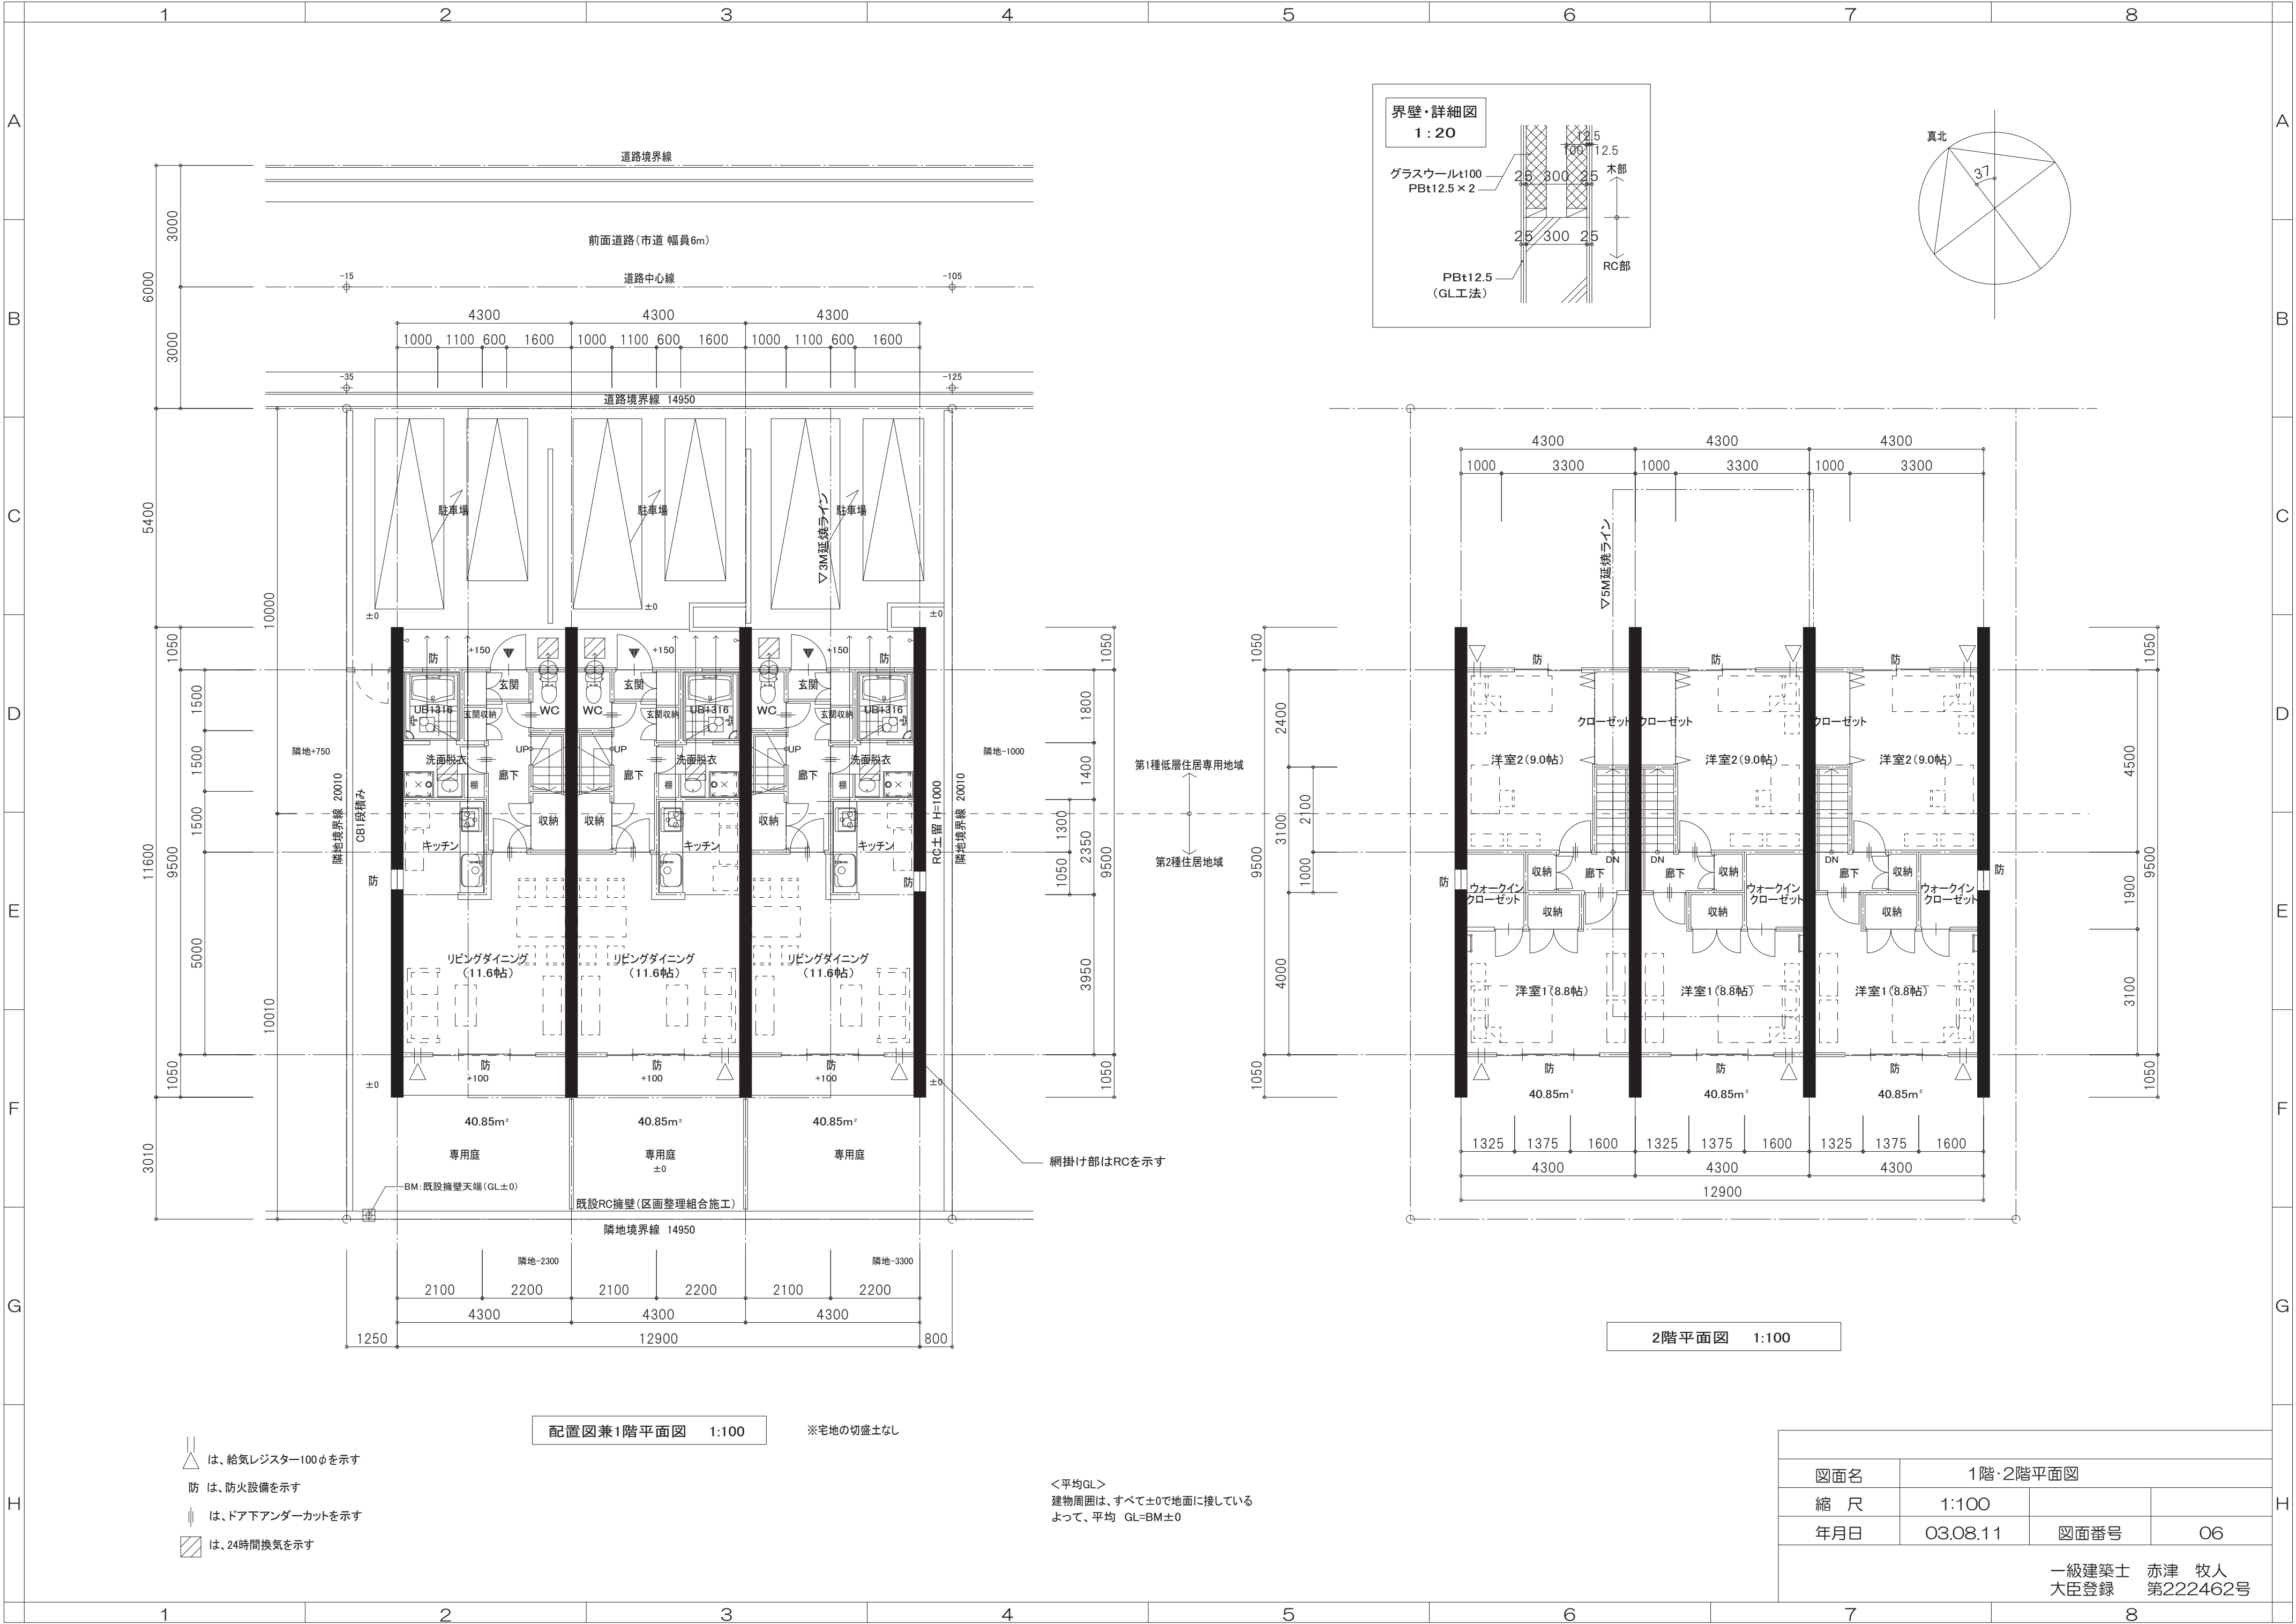

△ は、給気レジスター100φを示す  
防 は、防火設備を示す  
|| は、ドア下アンダーカットを示す  
斜線は、24時間換気を示す


配置図兼1階平面図 1:100

※宅地の切盛土なし

<平均GL>  
建物周囲は、すべて±0で地面に接している  
よって、平均 GL=BM±0

2階平面図 1:100

| 図面名                          |          |      |    |
|------------------------------|----------|------|----|
| 1階・2階平面図                     |          |      |    |
| 縮 尺                          | 1:100    |      |    |
| 年月日                          | 03.08.11 | 図面番号 | 06 |
| 一級建築士 赤津 牧人<br>大臣登録 第222462号 |          |      |    |

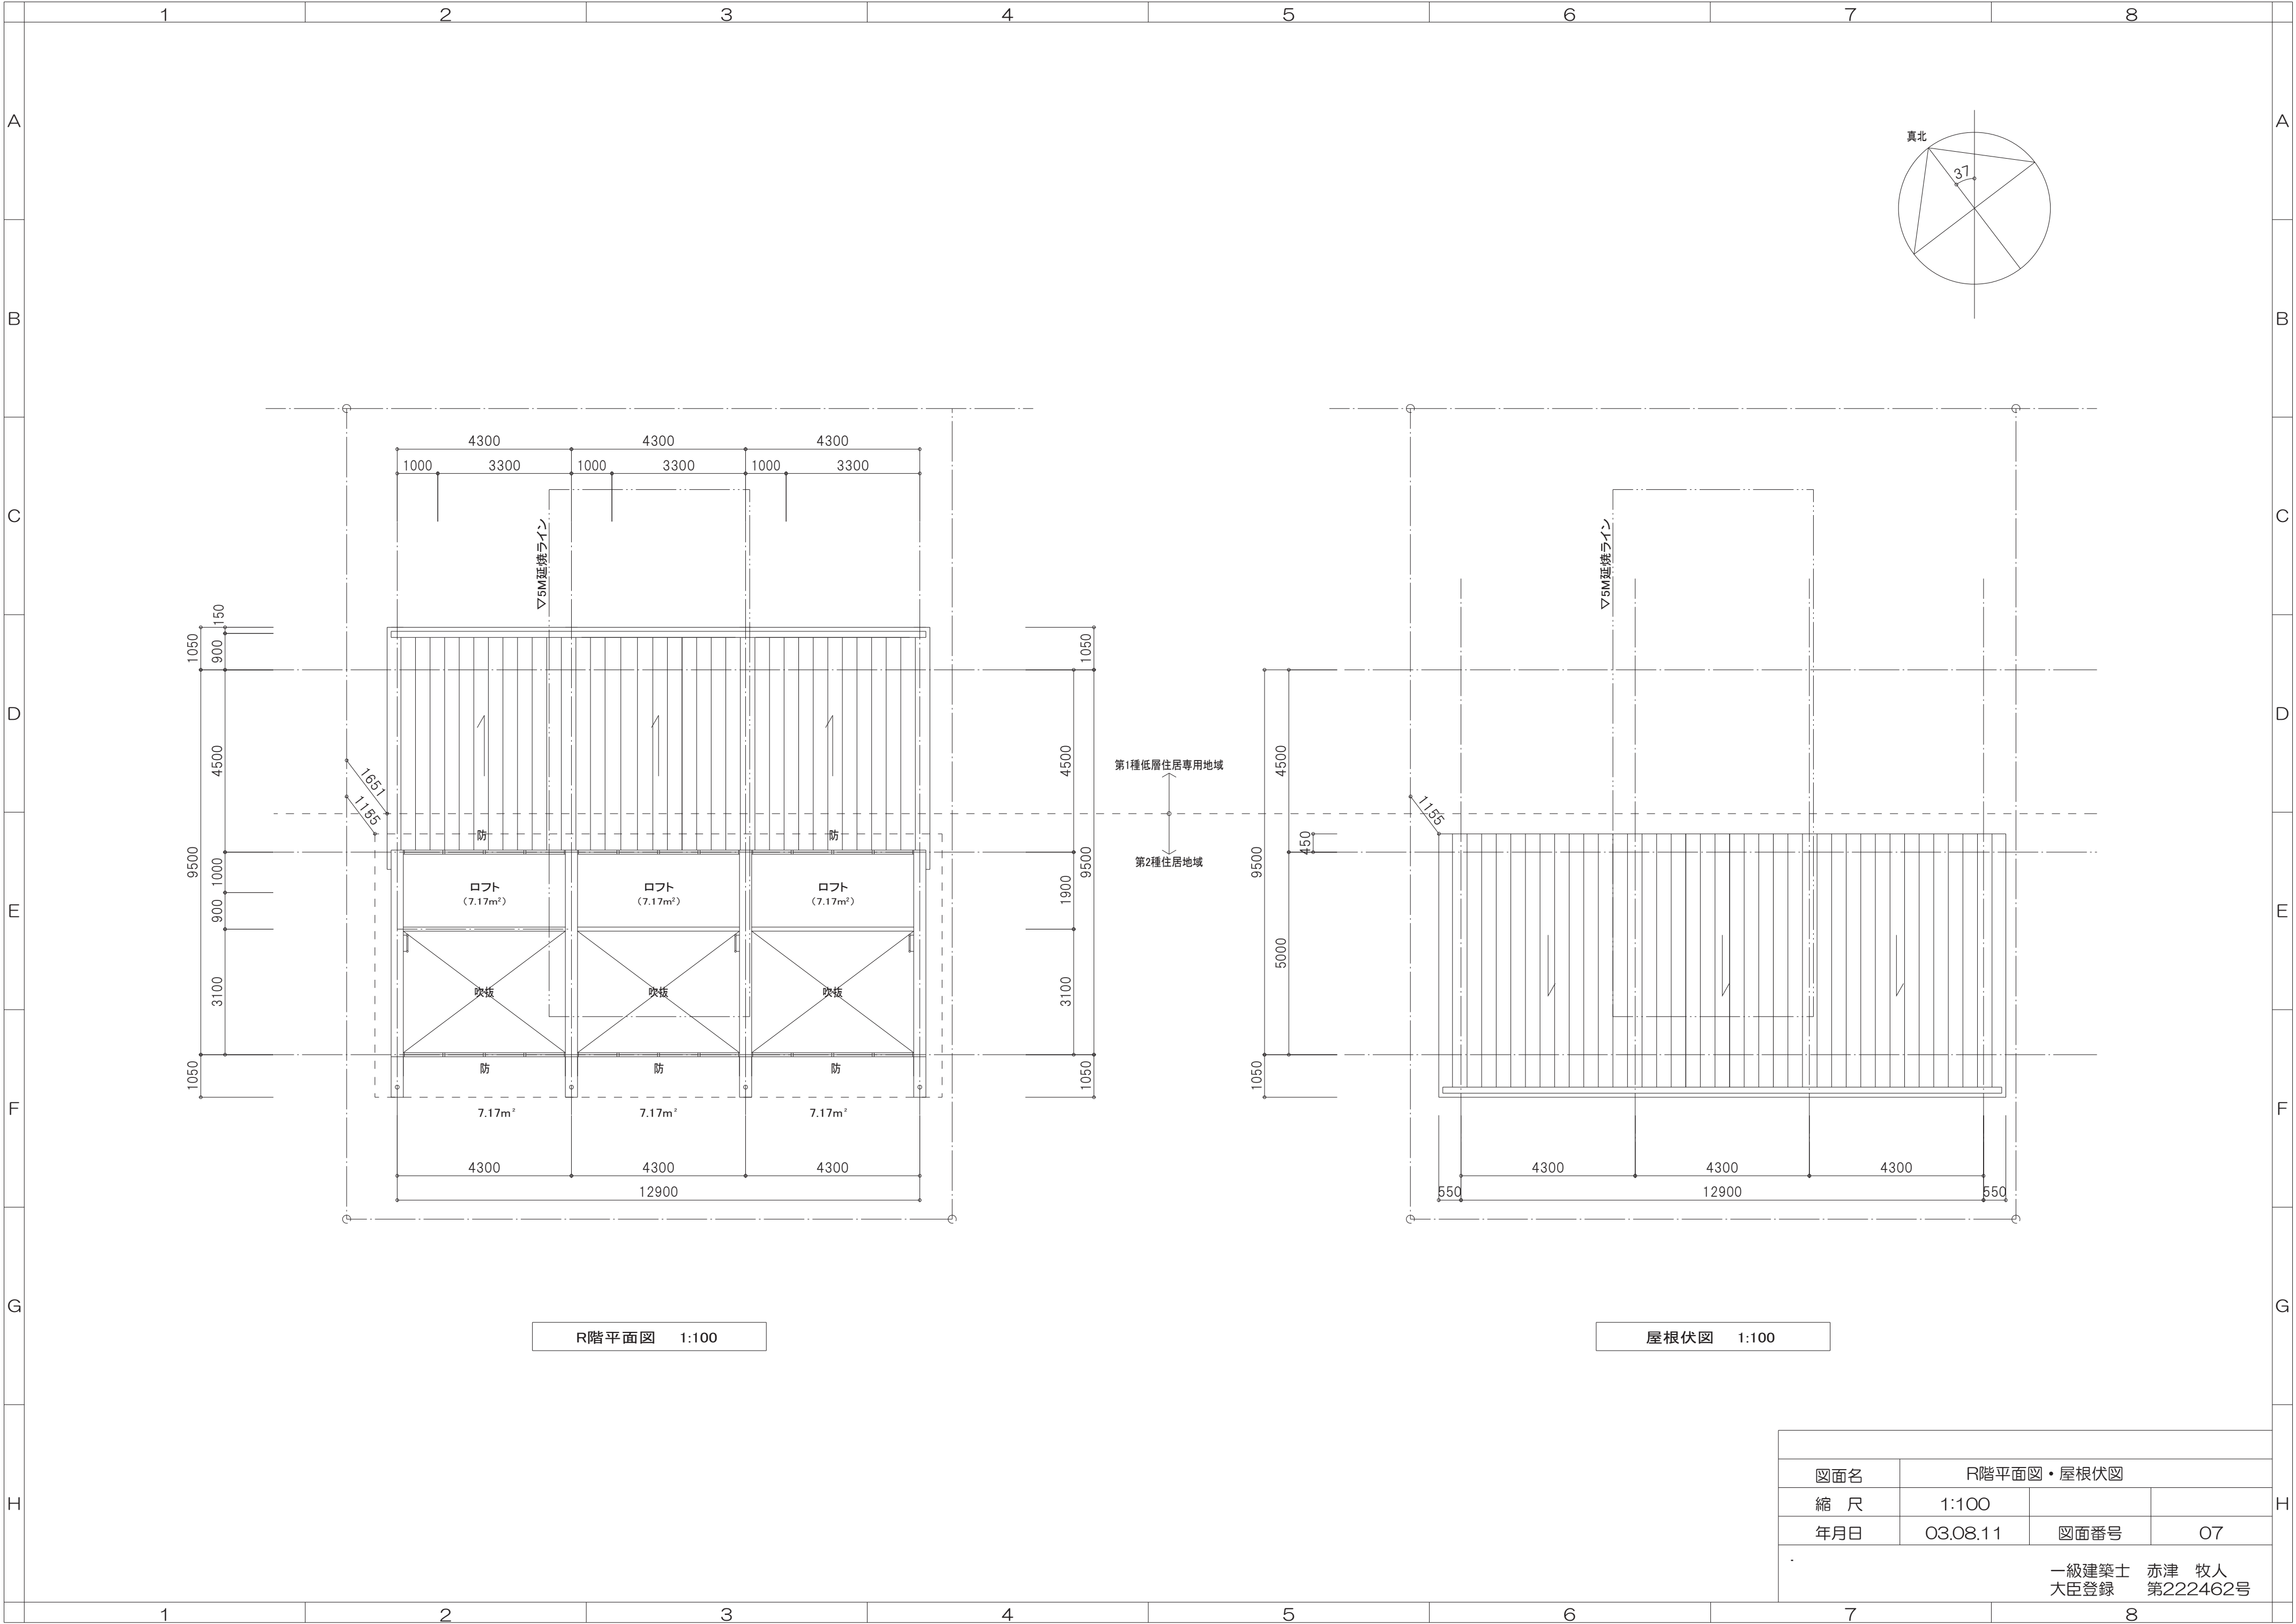


R階平面図 1:100


屋根伏図 1:100

|     |  |          |  |                              |  |
|-----|--|----------|--|------------------------------|--|
| 図面名 |  |          |  | R階平面図・屋根伏図                   |  |
| 縮 尺 |  | 1:100    |  |                              |  |
| 年月日 |  | 03.08.11 |  | 図面番号                         |  |
|     |  |          |  | 07                           |  |
|     |  |          |  | 一級建築士 赤津 牧人<br>大臣登録 第222462号 |  |



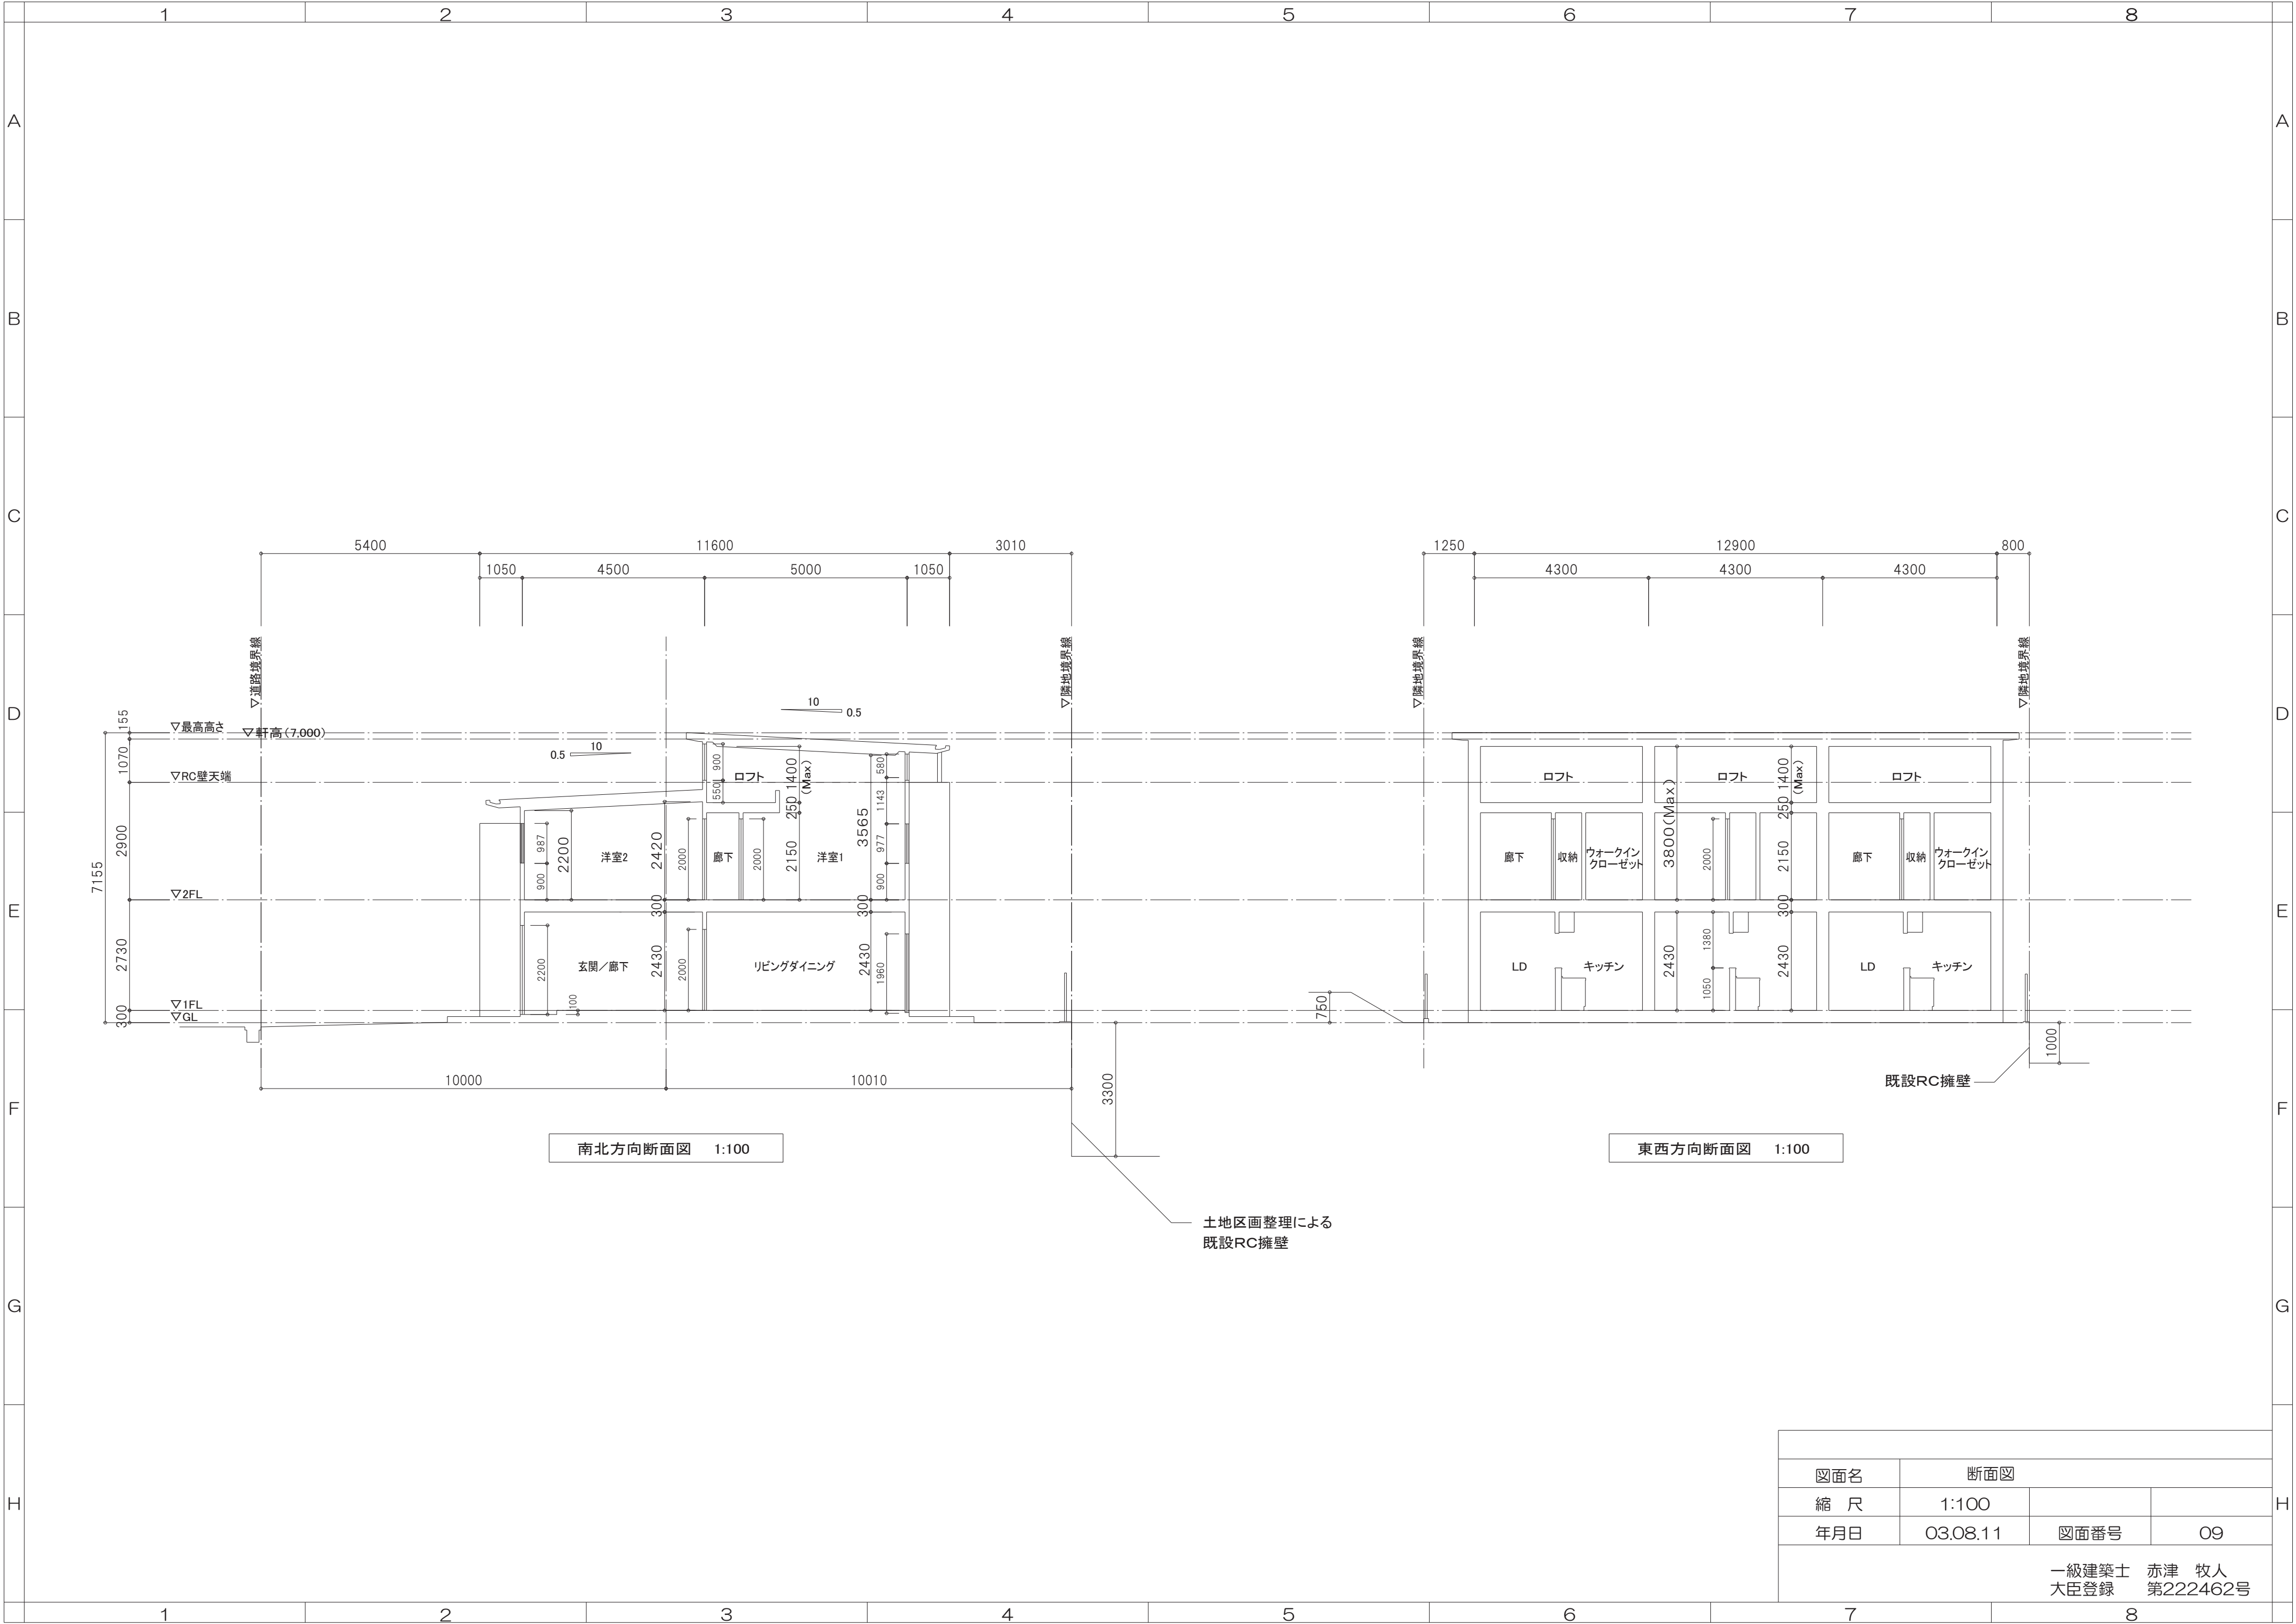

| 図面名                          |          | 断面図  |    |
|------------------------------|----------|------|----|
| 縮 尺                          | 1:100    |      |    |
| 年月日                          | 03.08.11 | 図面番号 | 09 |
| 一級建築士 赤津 牧人<br>大臣登録 第222462号 |          |      |    |

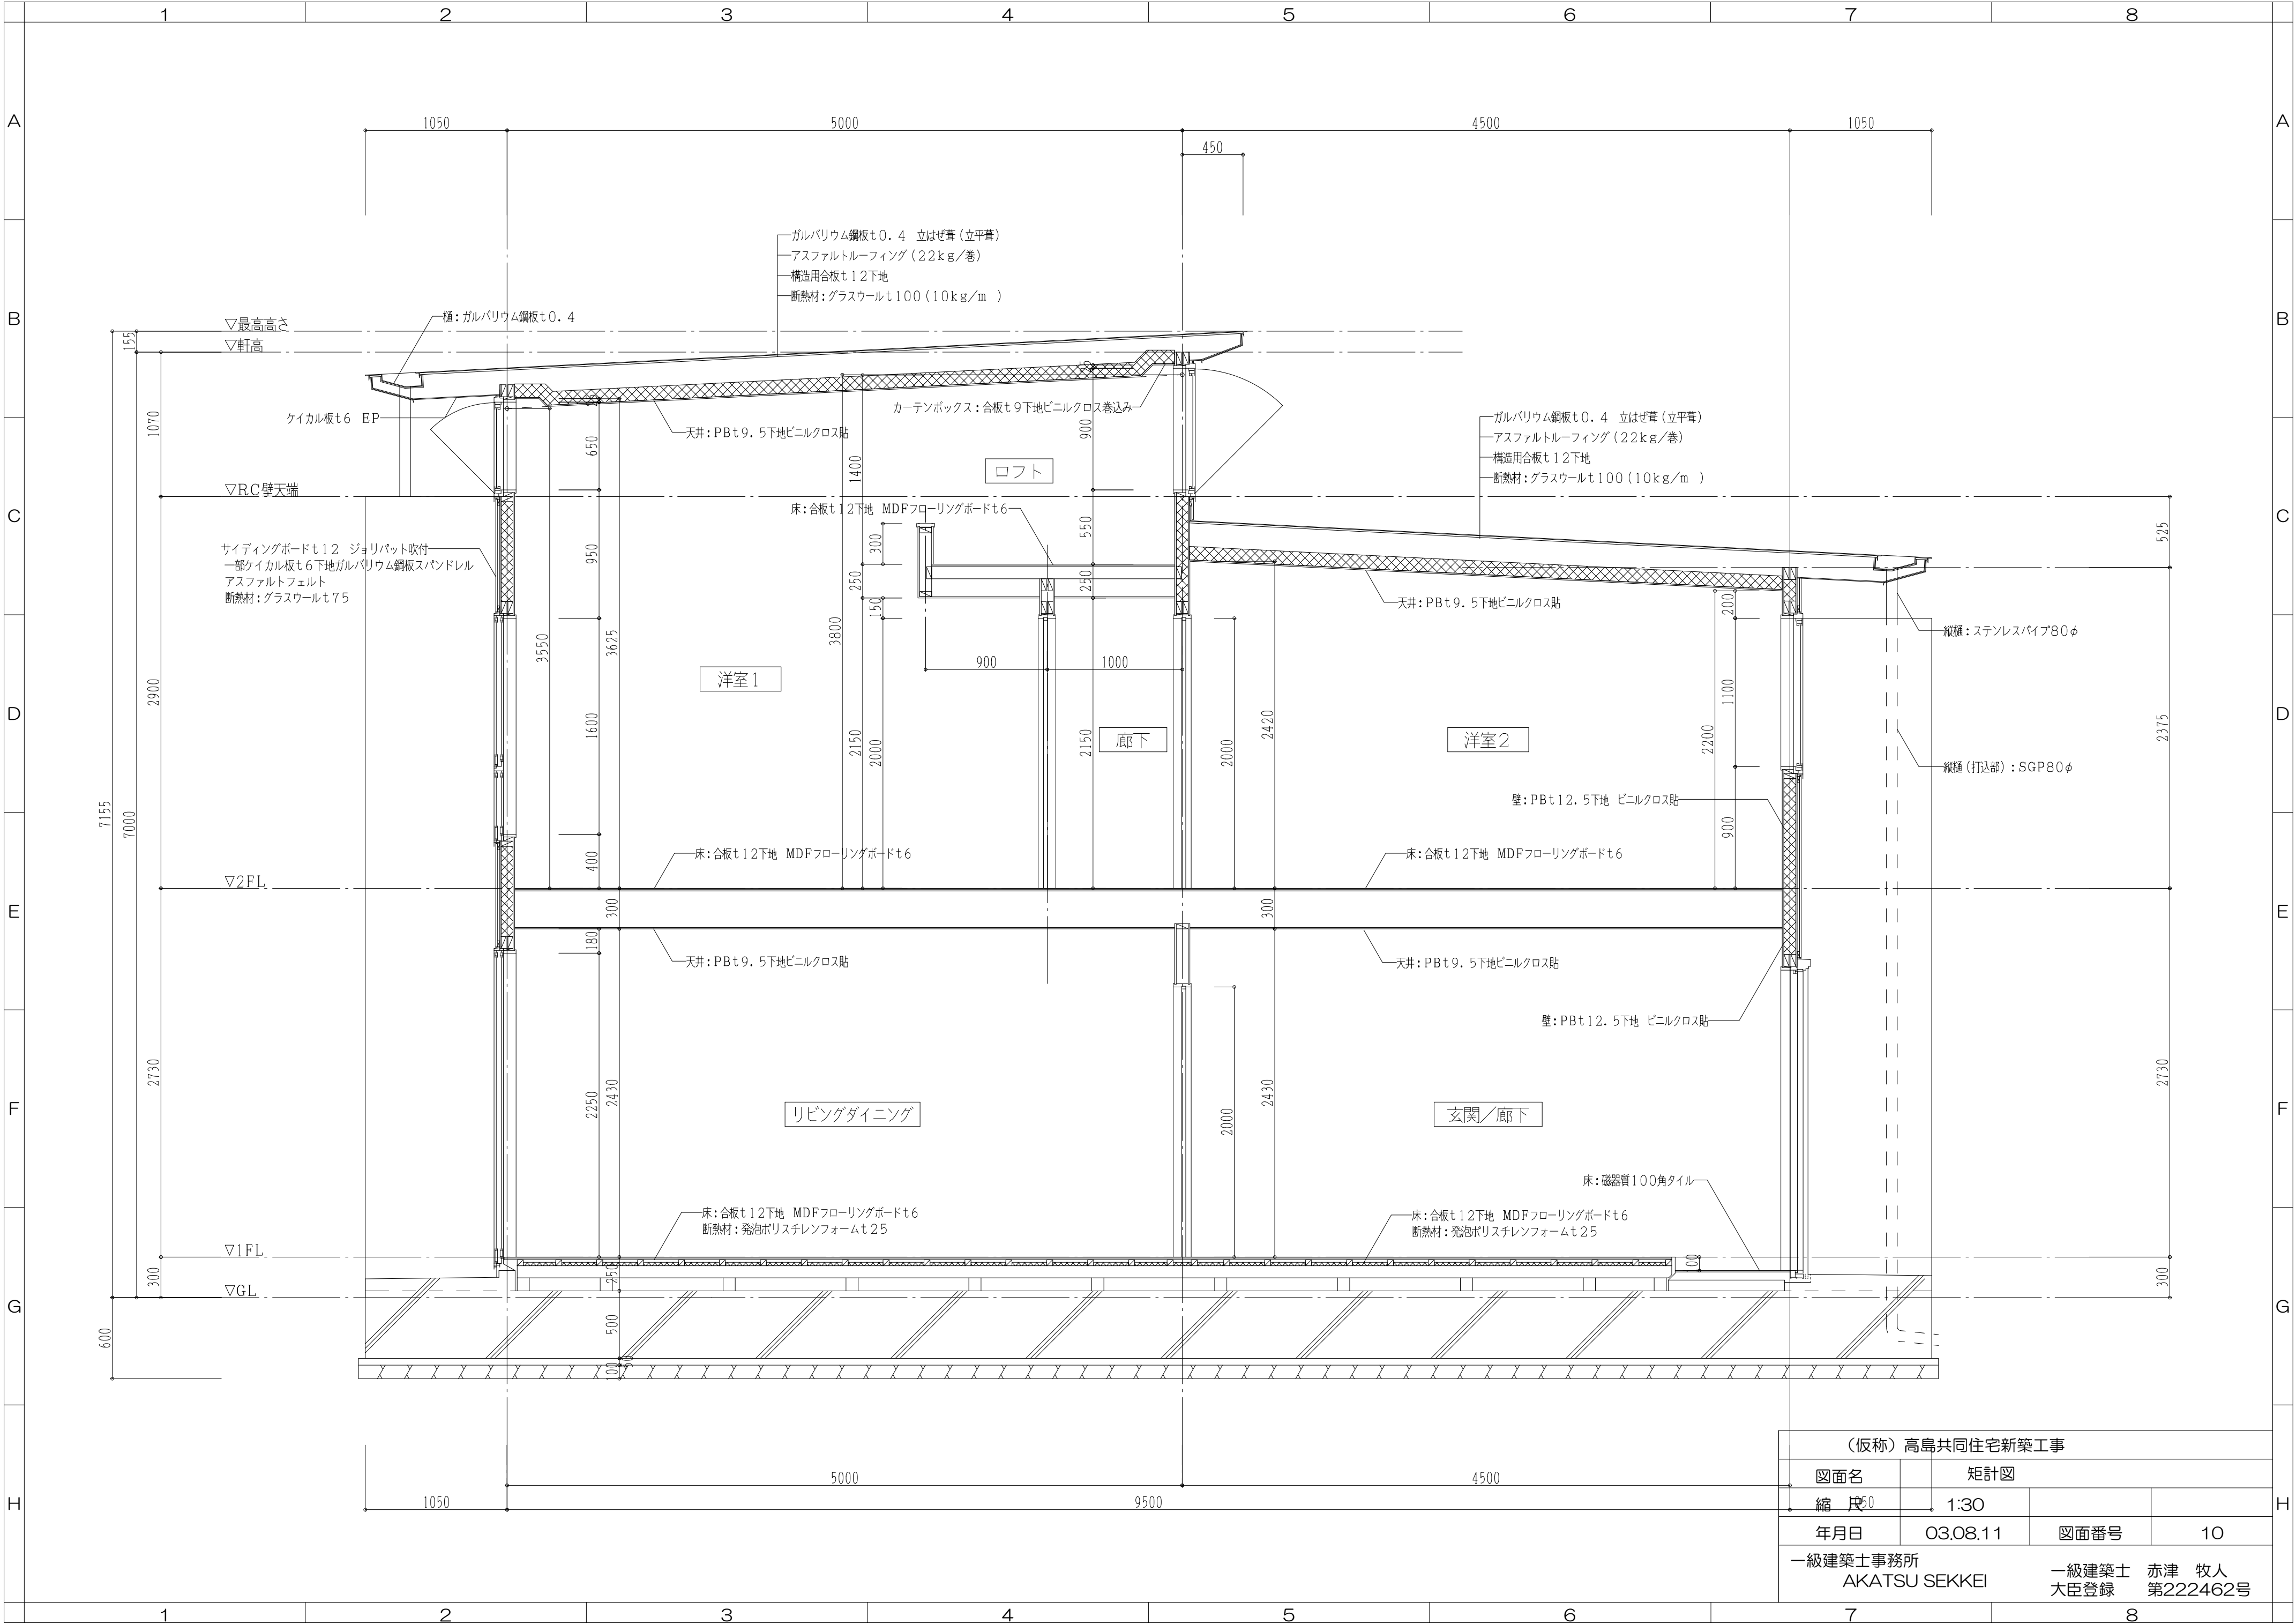

|                           |          |               |                   |
|---------------------------|----------|---------------|-------------------|
| （仮称）高島共同住宅新築工事            |          |               |                   |
| 図面名                       | 矩計図      |               |                   |
| 縮尺                        | 1:30     | 図面番号          | 10                |
| 年月日                       | 03.08.11 | 図面番号          | 10                |
| 一級建築士事務所<br>AKATSU SEKKEI |          | 一級建築士<br>大臣登録 | 赤津 牧人<br>第222462号 |





