

A

B

C

D

E

F

G

H

1

2

3

4

5

6

7

8

建築概要

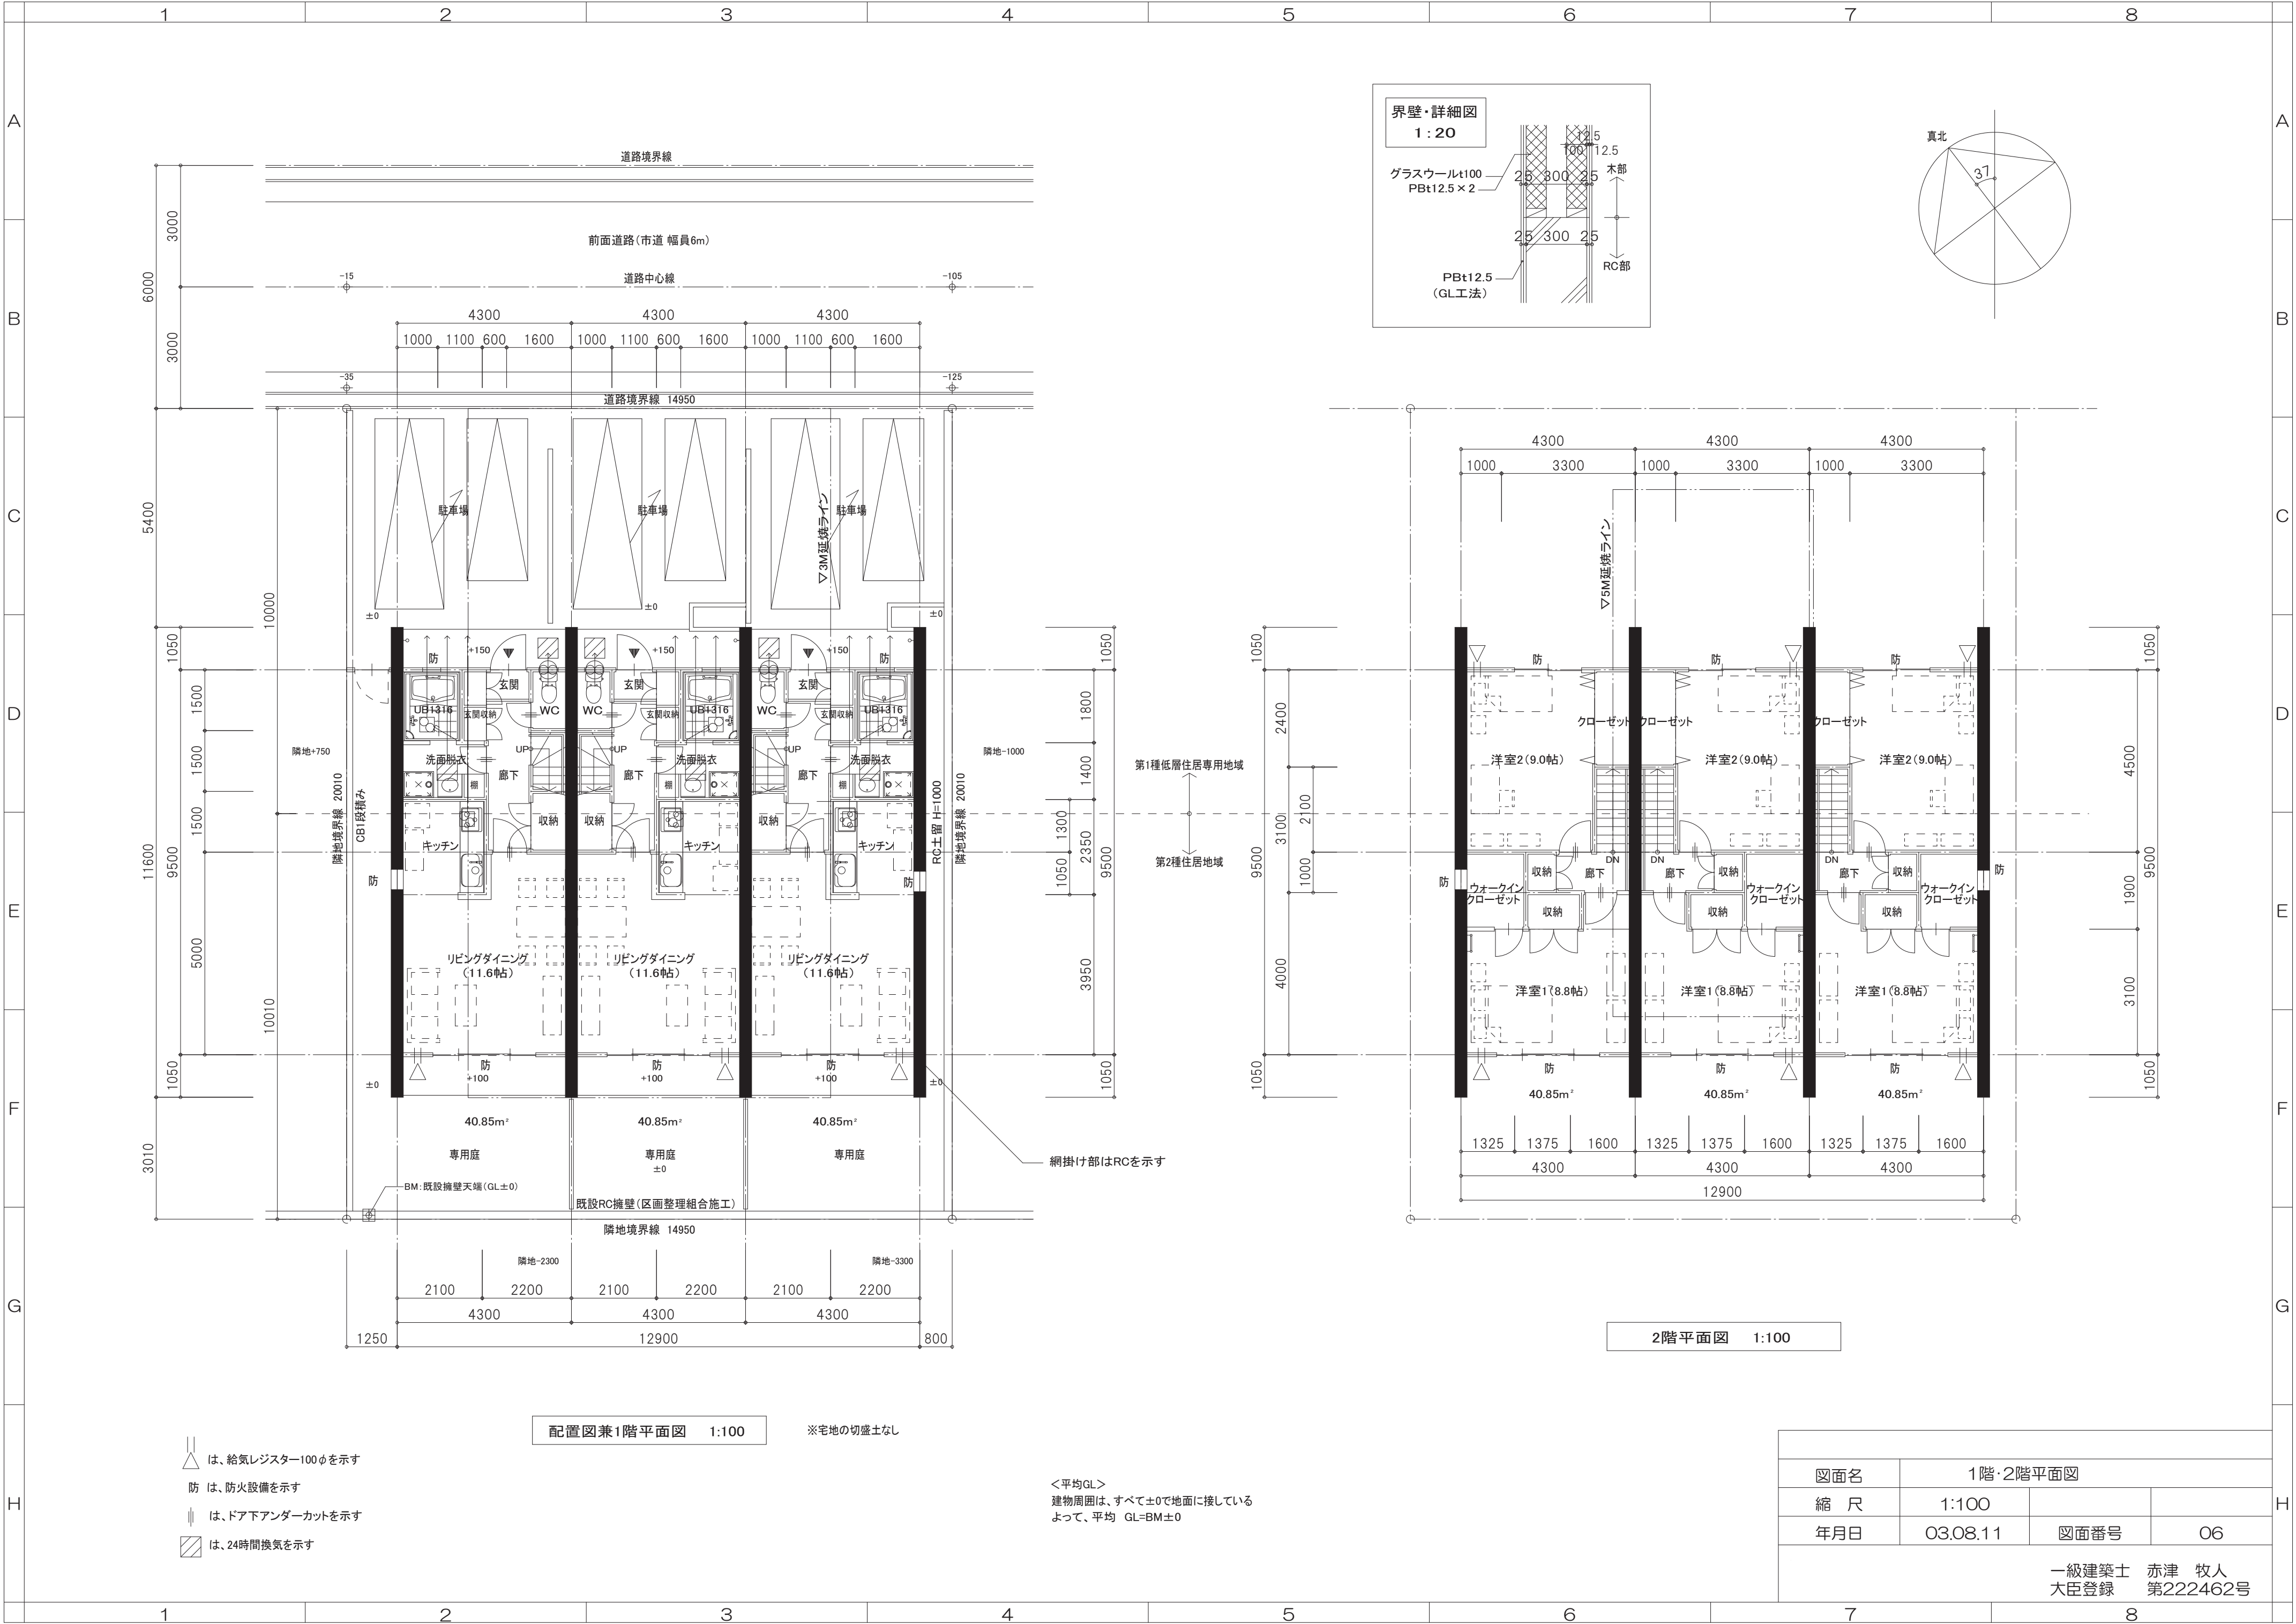
物件名		用途地域	第1種低層住居専用地域・第2種住居地域		
所在地		防火地域	指定無し		
敷地面積	299.21 m ² (90.52坪)	その他の地域・地区	10m高度地区・20m高度地区		
構造・規模	鉄筋コンクリート造+木造(混構造) 2階建て		宅地造成等規制区域		
建築面積	123.20 m ² (37.27坪) 建蔽率 41.18%				
延床面積	245.10 m ² (74.14坪) 容積率 81.92%	前面道路	北:6m		
	1階:122.55m ² 2階:122.55m ²	建ぺい率	50%・60%		
施工床面積	296.7 m ² (89.75坪)	容積率	150%・200%		

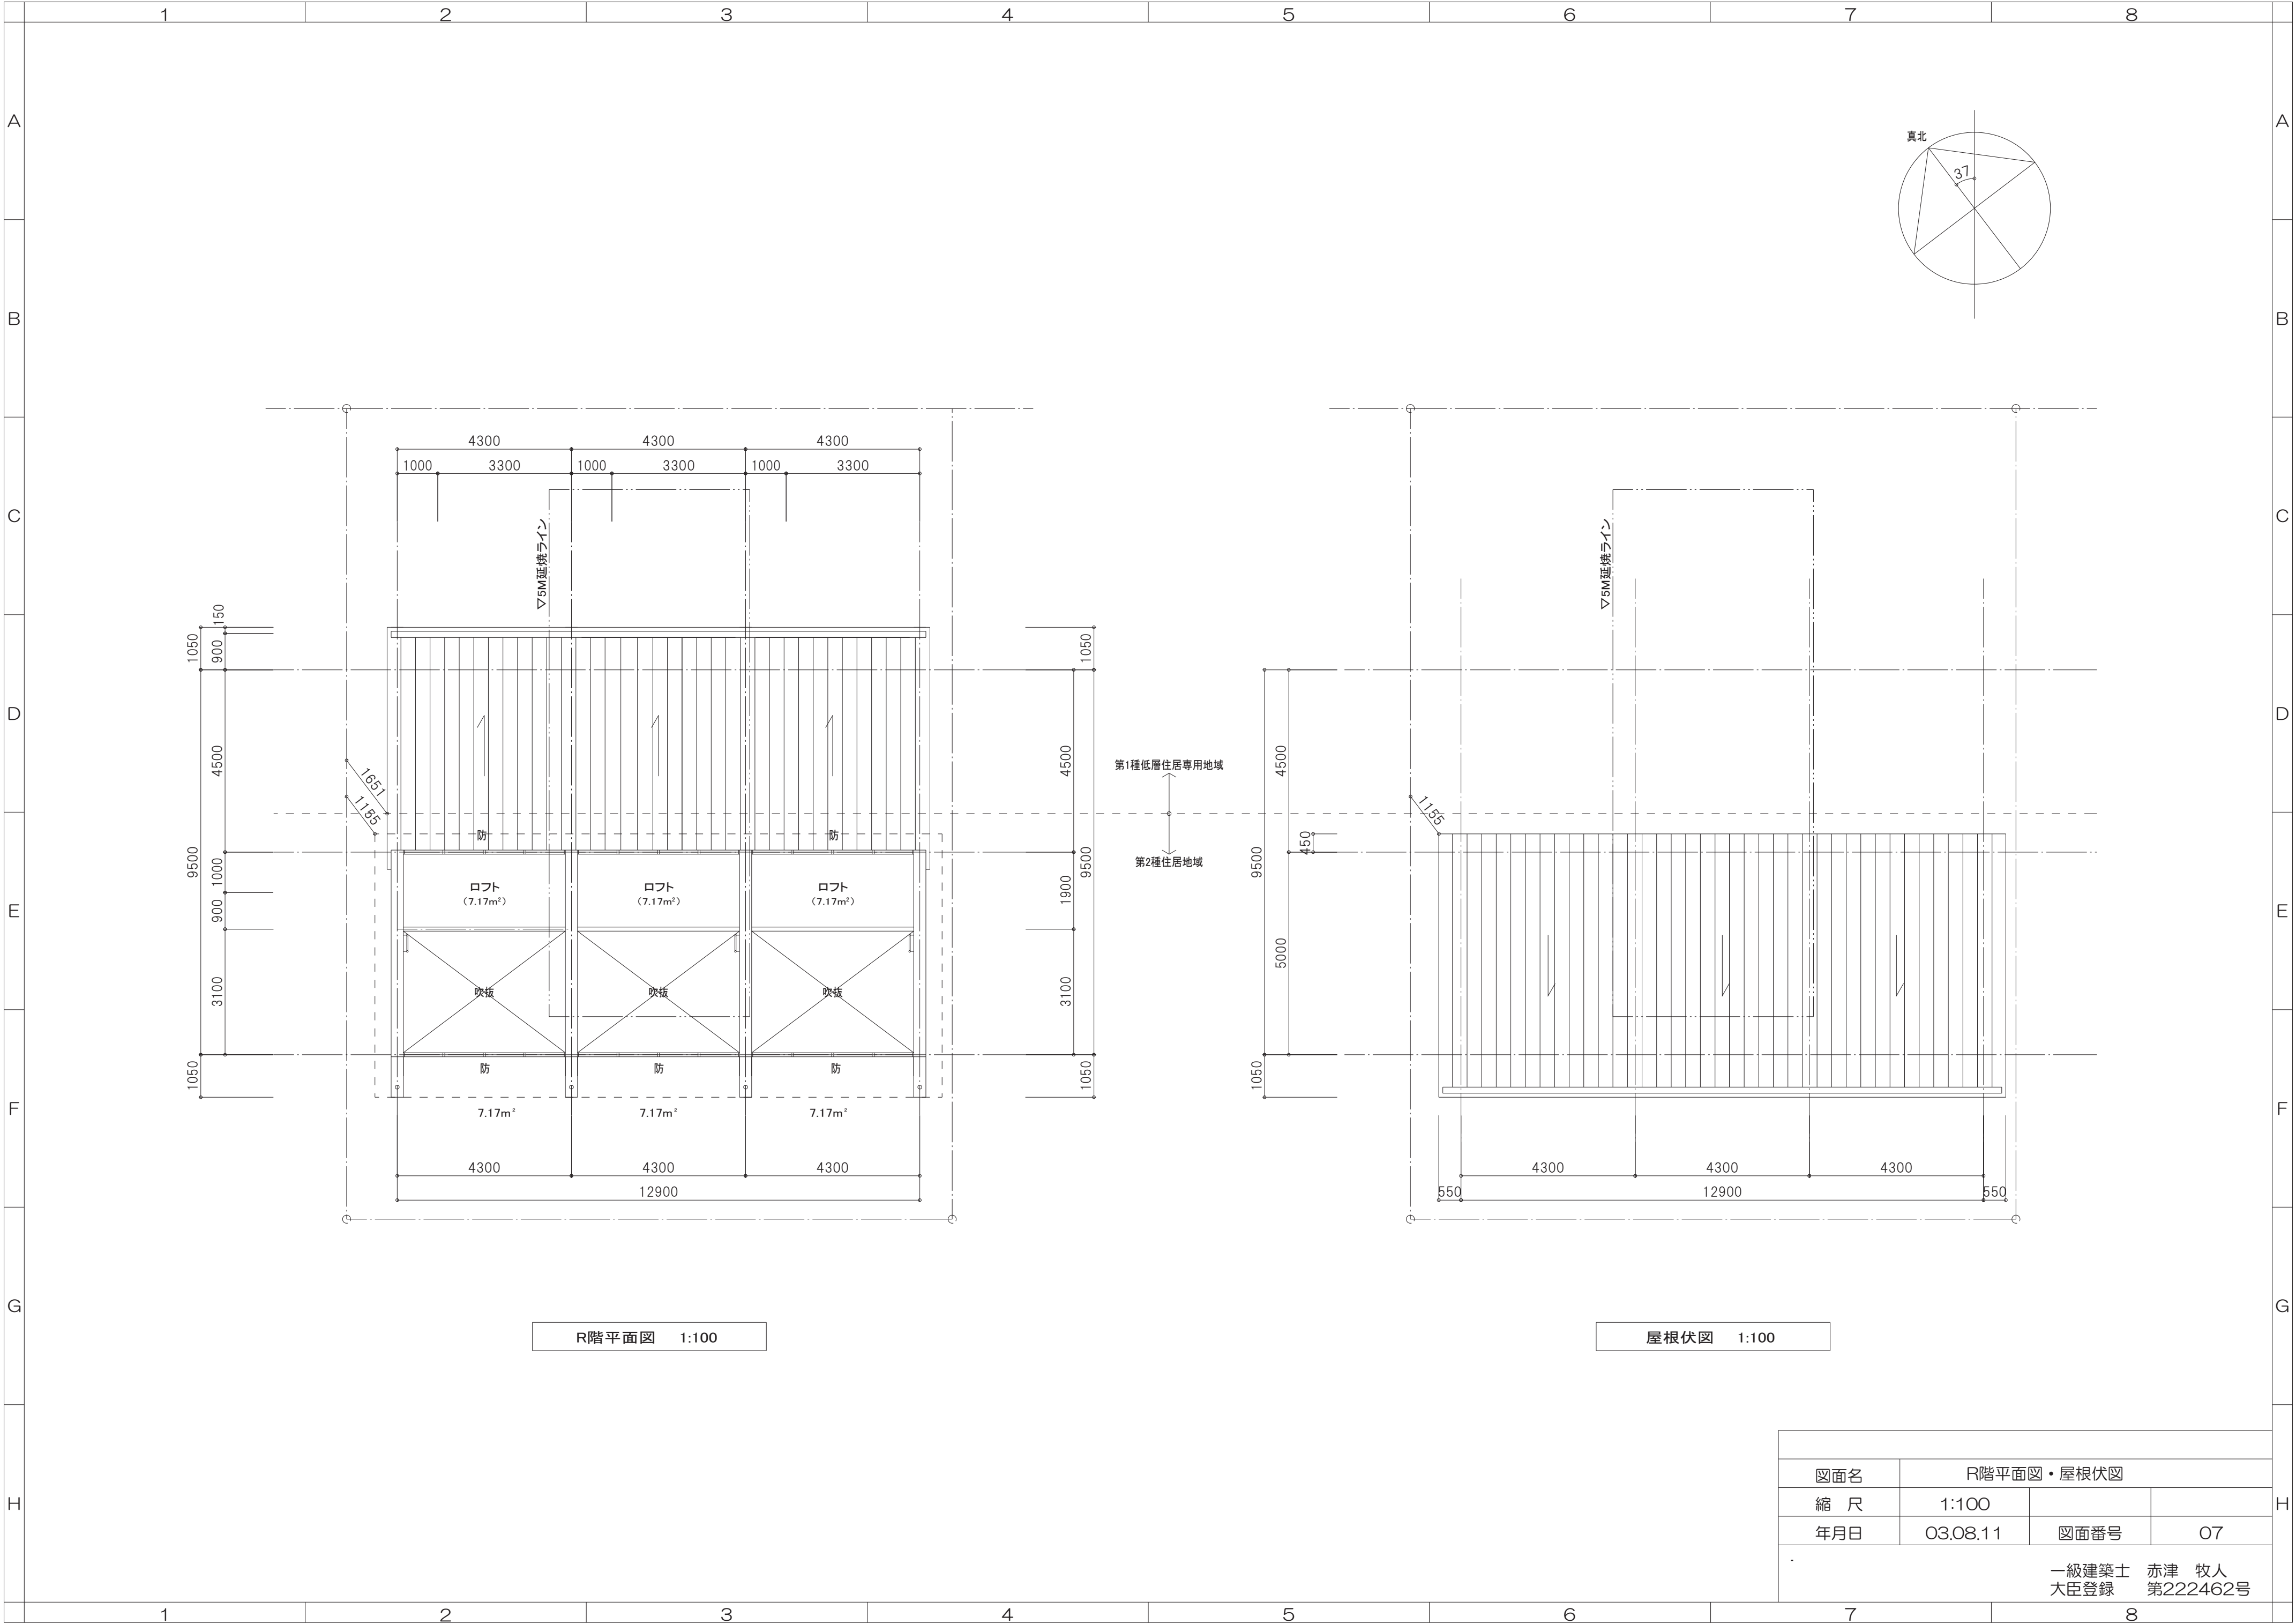
外部仕上表

屋根	ガルバリウム鋼板t0.4 立はぜ葺(立平葺)	テラス・ポーチ床	コンクリートコテ仕上げ		
	アスファルトルーフィング(22kg/巻)+合板t12下地	軒天井	珪酸カルシウム板t6 EP		
	断熱材:グラスウールt100(10kg/m ³) ²	外部幅木	コンクリート打放し		
外壁1	コンクリート打放し フッ素樹脂クリアー 耐火	軒樋	ガルバリウム鋼板t0.4		
外壁2	耐水PBt12.5下地 ガルバリウム鋼板スパンドレル張	縦樋	ステンレスパイプ80φ		
告示1359号 第1-11(2)	断熱材:グラスウールt75(10kg/m ³) ²	水切り類	アルミ		
外壁3	セメント系サイディングボードt12下地 ジョリパット吹付 PCO30BE-9201	外部開口部	アルミサッシ		
	断熱材:グラスウールt75(10kg/m ³) ²				

内部仕上表

階	室名	天井高	床		幅木	壁		天井		備考
		床高	下地	仕上		下地	仕上	下地	仕上	
D	1 玄関	CH=2530 FL-100	モルタル	磁器質100角タイル	化粧MDF H=60	PBt12.5	ビニルクロス	PBt9.5	ビニルクロス	玄関収納
		CH=2430 FL±0	合板t12	MDFフローリングボードt6	↑	↑	↑	↑	↑	
	廊下	断熱材発泡ポリスチレンフォームt25								
		CH=2430 FL±0	↑	↑	↑	↑	↑	↑	↑	カーテンレール
	リビングダイニング	CH=2430 FL±0	↑	↑	↑	耐水PBt12.5	ビニルクロス(QM-9416)	PBt9.5	ビニルクロス(QM-9416)	流し台:L=2250 レンジフード:L=600 吊戸棚:H=500,W=900+750
		CH=2430 FL±0	↑	↑	↑		一部化粧ケイカル板t6			棚:木製OP
	キッチン	CH=2230 FL±0	合板t12	クッションフロアt2.0	軟質ビニル幅木 H=60	耐水PBt12.5	ビニルクロス	PBt9.5	ビニルクロス	洗面化粧台:L=600 洗濯機パン:W=750 タオル掛:L=500
E	洗面脱衣	断熱材発泡ポリスチレンフォームt25								棚:塩ビシート貼
		CH=2230 FL±0	↑	↑	↑	↑	↑	↑	↑	ペーパーホルダー タオル掛 棚:木製OP
	WC	CH=2230 FL±0	↑	↑	↑	↑	↑	↑	↑	
		CH=2150 FL±0	合板t12	MDFフローリングボードt6	化粧MDF H=60	PBt12.5	ビニルクロス	↑	↑	
	2 廊下	CH=3300 FL±0	↑	↑	↑	↑	↑	↑	↑	カーテンレール
		CH=2310 FL±0	↑	↑	↑	↑	↑	↑	↑	カーテンレール
	洋室1	CH=2150 FL±0	↑	↑	↑	↑	↑	↑	↑	ハンガーパイプ 東側室のみカーテンレール
F	洋室2	CH=1400 FL±0	↑	↑	↑	↑	↑	↑	↑	
		R ロフト								
	共通 階段	CH=1400 FL±0		化粧LVL	化粧LVL	↑	↑	↑	↑	木製手すり
	収納		合板t12	MDFフローリングボードt6	雑巾摺り	PBt9.5	ビニルクロス	↑	↑	クローゼットにはハンガーパイプ
G										
H	不燃・準不燃リスト									
		PBt12.5 NM-8619								






R階平面図 1:100

屋根伏図 1:100


図面名				R階平面図・屋根伏図	
縮 尺		1:100			
年月日		03.08.11		図面番号	
				07	
				一級建築士 赤津 牧人 大臣登録 第222462号	














立面図			
図面名	立面図		
縮 尺	1:100		
年月日	03.08.11	図面番号	08
一級建築士 赤津 牧人 第222462号			

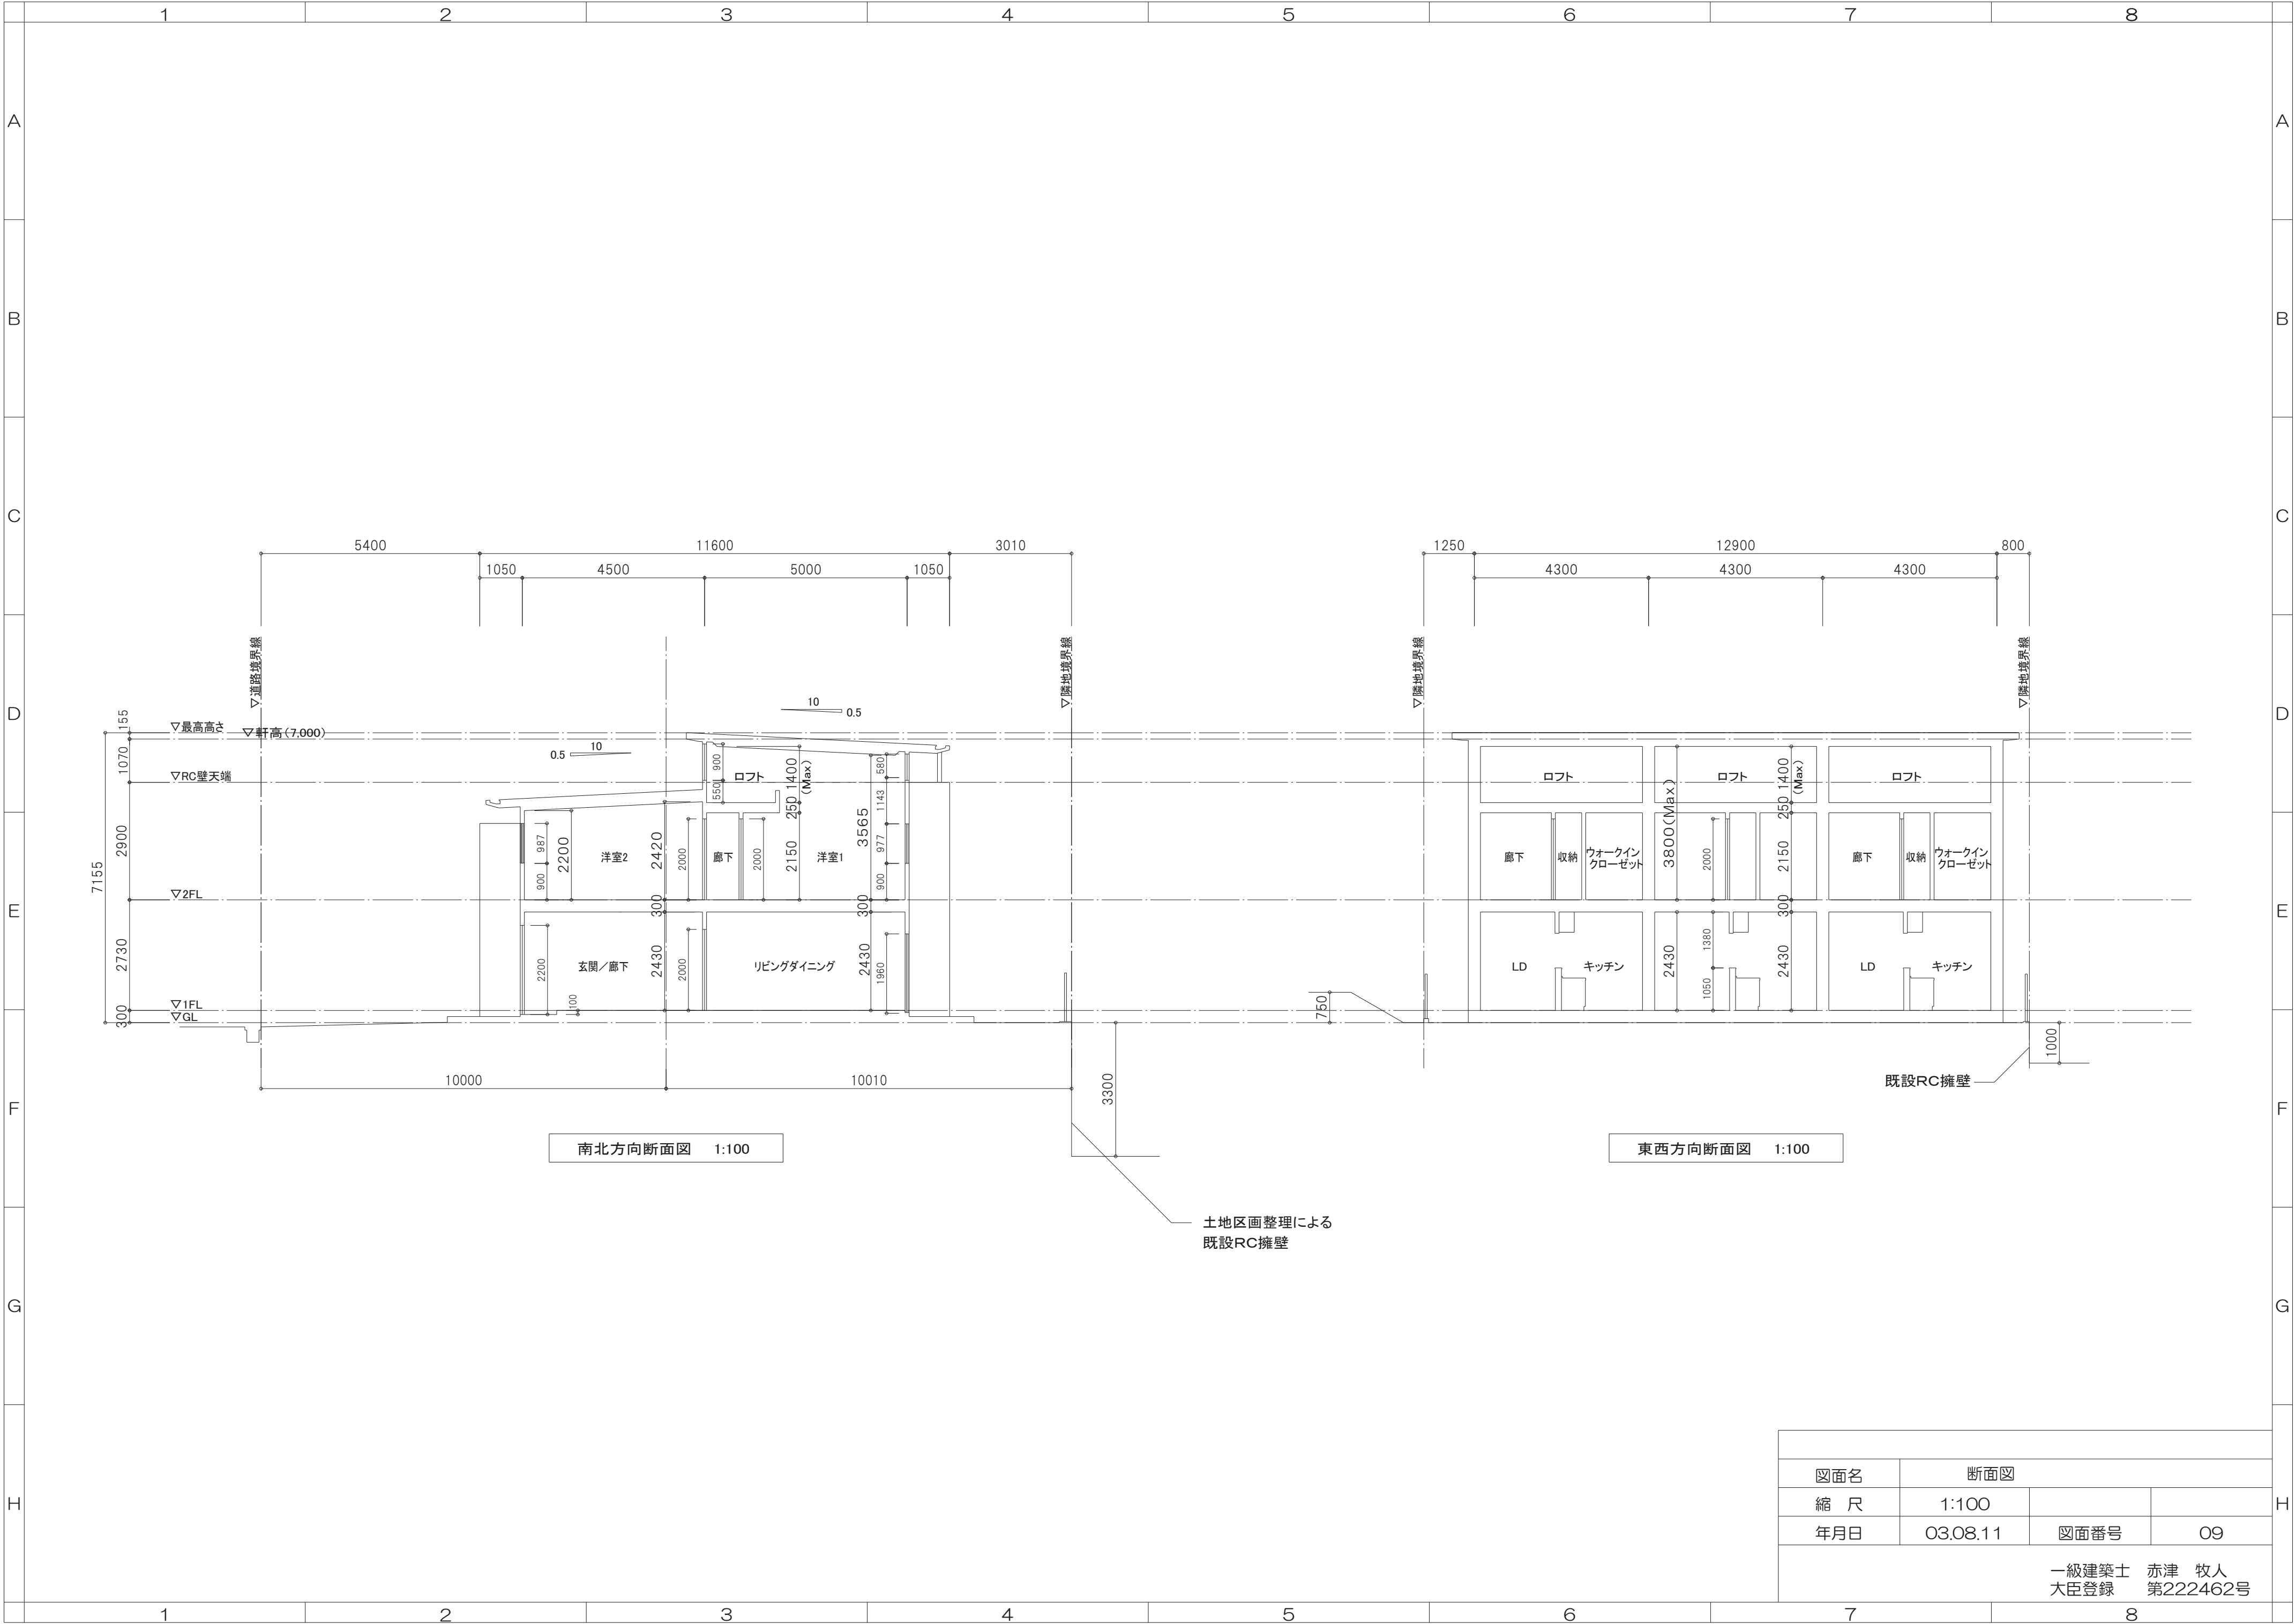

図面名		断面図	
縮 尺	1:100		
年月日	03.08.11	図面番号	09
一級建築士 赤津 牧人 第222462号			

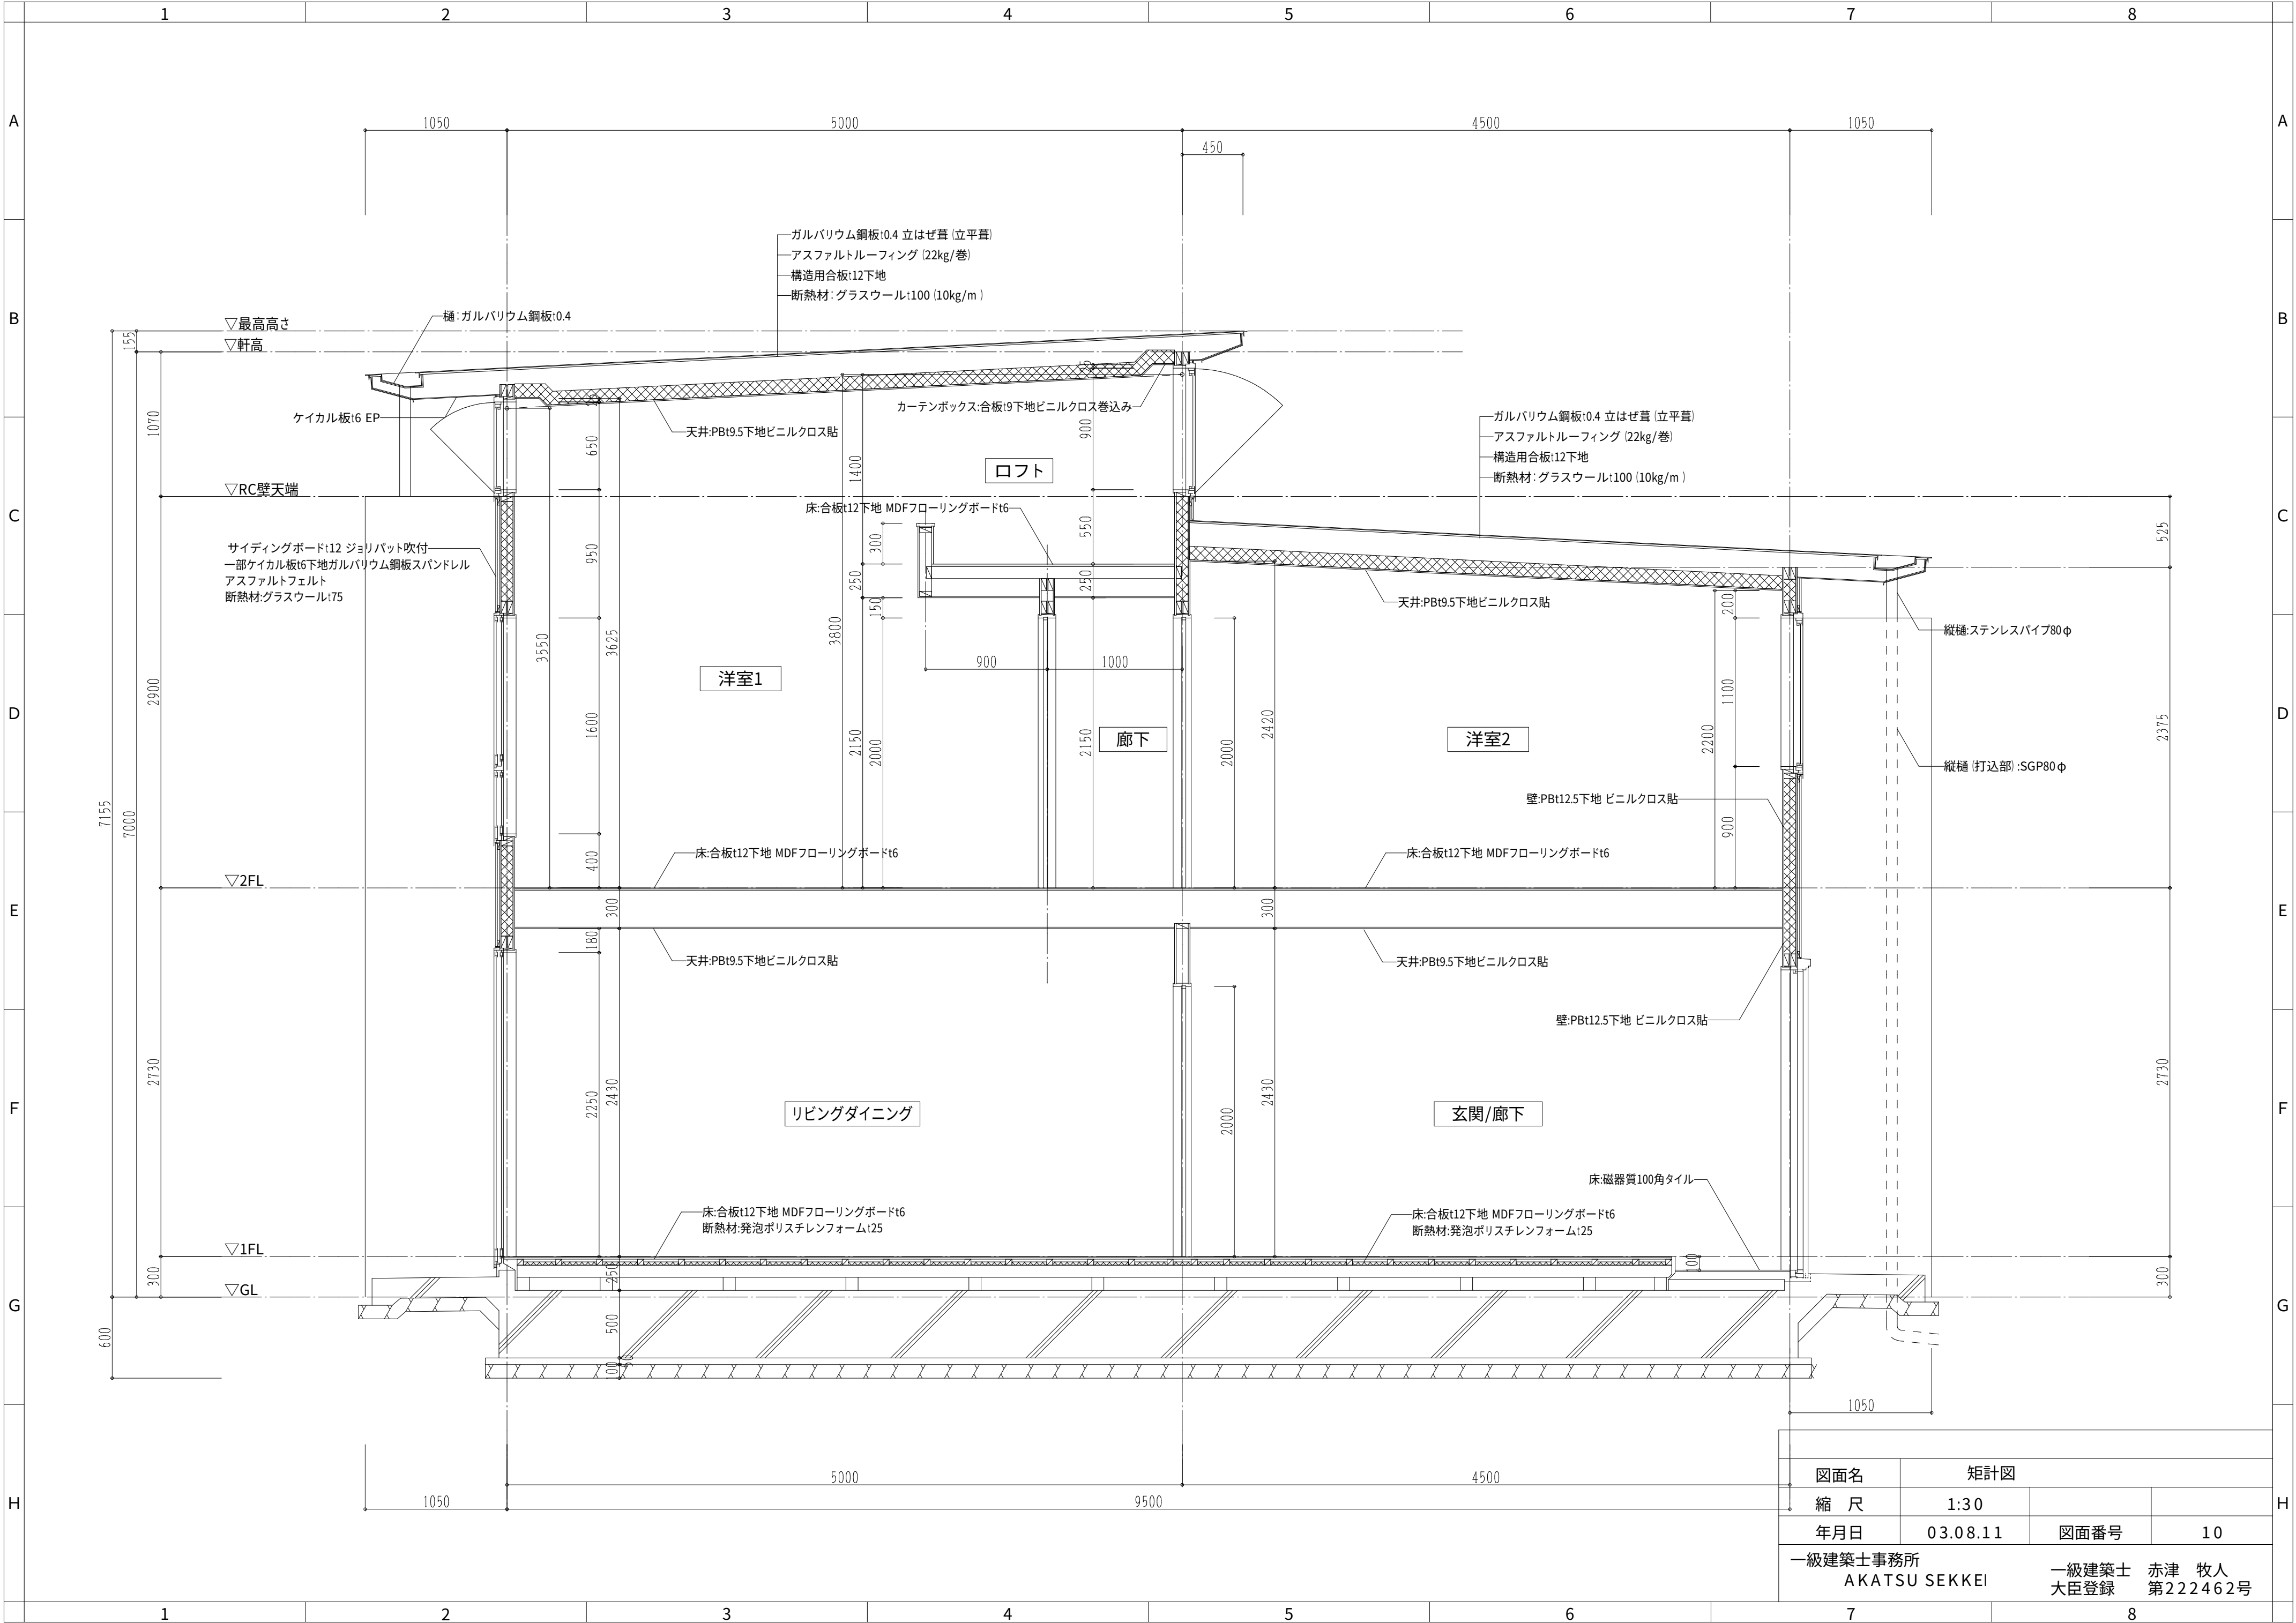


図面名		矩計図	
縮 尺	1:30		
年月日	03.08.11	図面番号	10
一級建築士事務所 AKATSU SEKKEI		一級建築士 大臣登録	赤津 牧人 第222462号

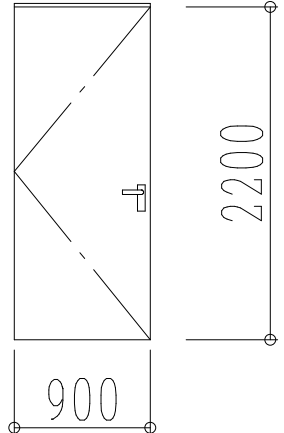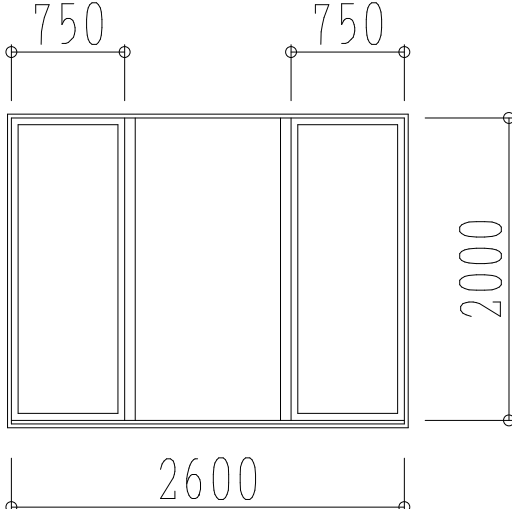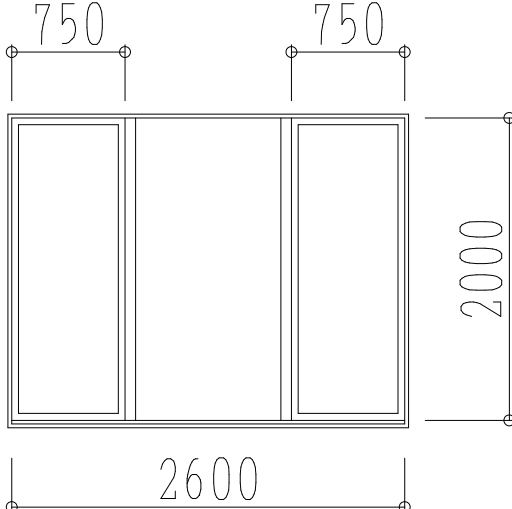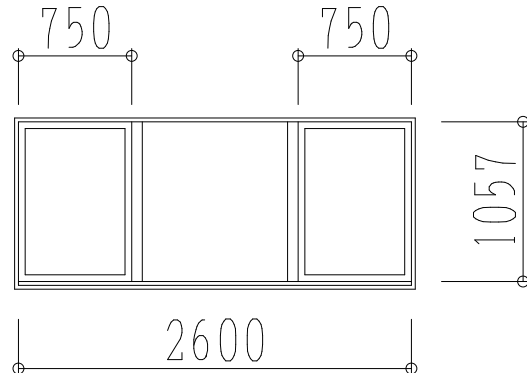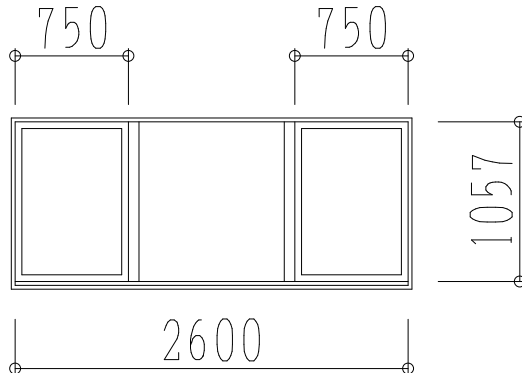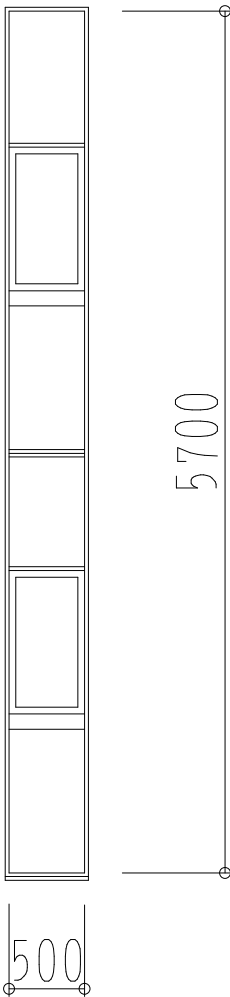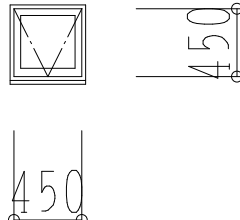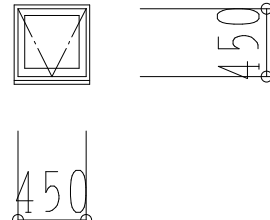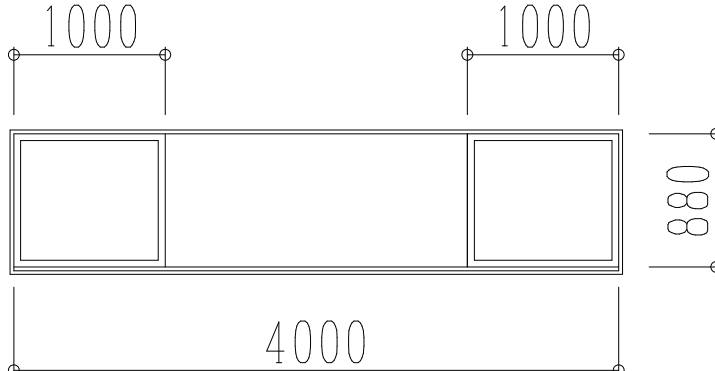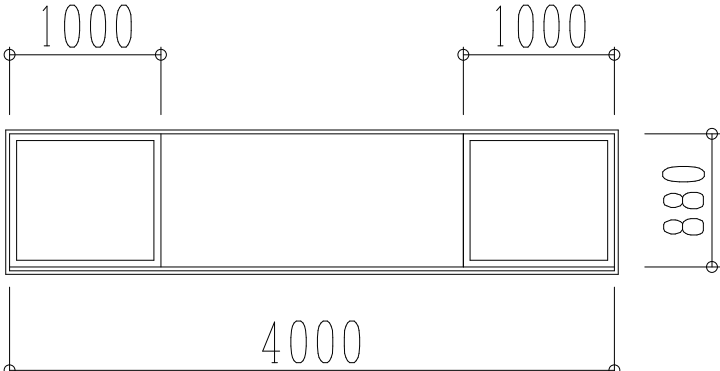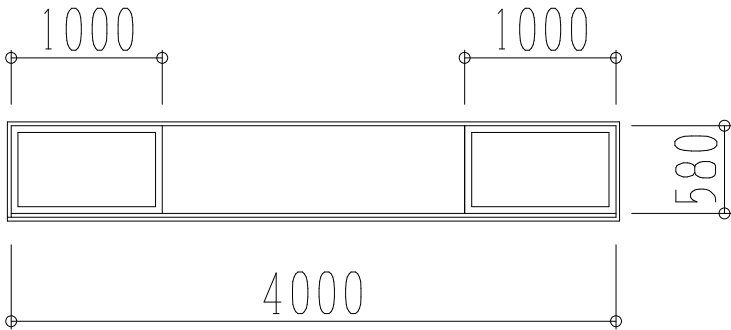		1		2		3		4		5		6		7		8						
		符号・名称	1SD 片開き鋼製ドア	乙防	1AW ハメ殺し+引違いアルミサッシ (欄間付)	乙防	2AW ハメ殺し+引違いアルミサッシ (欄間付)		3AW ハメ殺し+引違いアルミサッシ (欄間付)	乙防	4AW ハメ殺し+引違いアルミサッシ (欄間付)											
A	姿図・寸法																A					
B																	B					
		見込・場所・数量	70	玄関	3	70	リビングダイニング (11.6帖)	2	70	リビングダイニング (11.6帖)	1	70	洋室1 (8.8帖)・洋室2 (9.0帖)	5	70	洋室1 (8.8帖)・洋室2 (9.0帖)	1					
C	仕 上	化粧鋼板				アルミ ステンレスカラー				アルミ ステンレスカラー				アルミ ステンレスカラー								
	ガ ラ ス					網入り透明ガラスt6.8				透明ガラスt5				網入り透明ガラスt6.8				透明ガラスt5				
	金 物	付属金物一式・ドアチェック・シリンダー錠・ステンレスレバーハンドル・フランス落とし				付属金物一式				付属金物一式				付属金物一式				付属金物一式				
	備 考	下枠ステンレス <TOSTEMU MDシリーズ OM3程度>				下枠ステンレス・網戸				下枠ステンレス・網戸				下枠ステンレス・網戸				下枠ステンレス・網戸				
	符号・名称	5AW ハメ殺し+横すべり出しアルミサッシ	乙防	6AW 内倒しアルミサッシ	乙防	7AW 内倒しアルミサッシ		8AW 横すべり出しアルミサッシ	乙防	9AW 横すべり出しアルミサッシ												
D	姿図・寸法																					D
E	見込・場所・数量					70	WC・浴室		2	70	WC・浴室		4	70	ロフト		3	70	ロフト		1	E
F	仕 上					アルミ ステンレスカラー				アルミ ステンレスカラー				アルミ ステンレスカラー				アルミ ステンレスカラー				
	ガ ラ ス					網入り透明ガラスt6.8				透明ガラスt5				網入型ガラスt6.8				透明ガラスt5				
	金 物					付属金物一式・アルミ水切				付属金物一式・アルミ水切				付属金物一式・アルミ水切				付属金物一式・アルミ水切				
	備 考					網戸・アルミ面格子				網戸・アルミ面格子				網戸・オペレーターハンドル				網戸・オペレーターハンドル				
	符号・名称					10AW 横すべり出しアルミサッシ	乙防	※乙防は防火設備を示す														
G	姿図・寸法																					
H		<外観図>				<外観図>																
	見込・場所・数量	70	リビングダイニング (11.6帖)	廊下	2	70	ロフト		3													
	仕 上	アルミ ステンレスカラー				アルミ ステンレスカラー																
	ガ ラ ス	網入り透明ガラスt6.8				網入型ガラスt6.8																
	金 物	付属金物一式・アルミ水切				付属金物一式・アルミ水切																
	備 考	下枠ステンレス・網戸				網戸・オペレーターハンドル																
	1		2		3		4		5		6		7		8							

		1		2		3		4		5		6		7		8	
		符号・名称	1WD 木製片開フラッシュ戸		2WD 木製両開フラッシュ戸		3WD 木製片開フラッシュ戸		4WD 木製片開フラッシュ戸		5WD 木製両開フラッシュ戸		6WD 木製両開フラッシュ戸		7WD 木製両開フラッシュ戸		
A		姿図・寸法															A
B																	
		見込・場所・数量	36	リビングダイニング (11.6帖)	3	36	1階 廊下	3	36	洗面所	3	36	WC	3	36	玄関	6
		仕 上	銘木合板t4 化粧合板t4			銘木合板t4			銘木合板t4			銘木合板t4			銘木合板t4		
		ガ ラ ス	透明ガラスt3														
C		金 物	ステンレス丁番・戸当り・ステンレスレバーハンドル・空錠			ステンレス取手			ステンレス丁番・戸当り・ステンレスレバーハンドル・空錠			ステンレス丁番・戸当り・ステンレスレバーハンドル・表示錠			ステンレス取手		
		備 考	木口テープ貼			木口テープ貼			木口テープ貼			木口テープ貼			木口テープ貼		
		符号・名称	6WD 木製両開フラッシュ戸		7WD 木製片開フラッシュ戸		8WD 木製片開フラッシュ戸		9WD 木製両開フラッシュ戸		10WD 木製両開フラッシュ戸		10WD 木製フラッシュハンガー折れ戸				
		姿図・寸法															D
D																	
E		見込・場所・数量	36	洋室1	3	36	洋室1	3	36	洋室1・洋室2	3	36	2階 廊下	3	36	洋室2	3
		仕 上	銘木合板t4			銘木合板t4			銘木合板t4			銘木合板t4			銘木合板t4		
		ガ ラ ス															
		金 物	ステンレス取手			ステンレス取手			ステンレス丁番・戸当り・ステンレスレバーハンドル・空錠			ステンレス取手			ナイロン戸車・ハンガーレール・ステンレス取手		
		備 考	木口テープ貼			木口テープ貼			木口テープ貼			木口テープ貼			木口テープ貼		
F																	
G																	
H																	
		1		2		3		4		5		6		7		8	

図面名				建具表 - 2			
縮 尺		1 : 50					
年月日		03.08.19		図面番号		12	
一級建築士事務所 AKATSU SEKKEI				一級建築士 赤津 牧人 大臣登録 第222462号			

図面名		建具表-2	
縮 尺	1 : 50		
年月日	03.08.19	図面番号	12
一級建築士事務所 AKATSU SEKKEI		一級建築士 大臣登録	赤津 牧人 第222462号

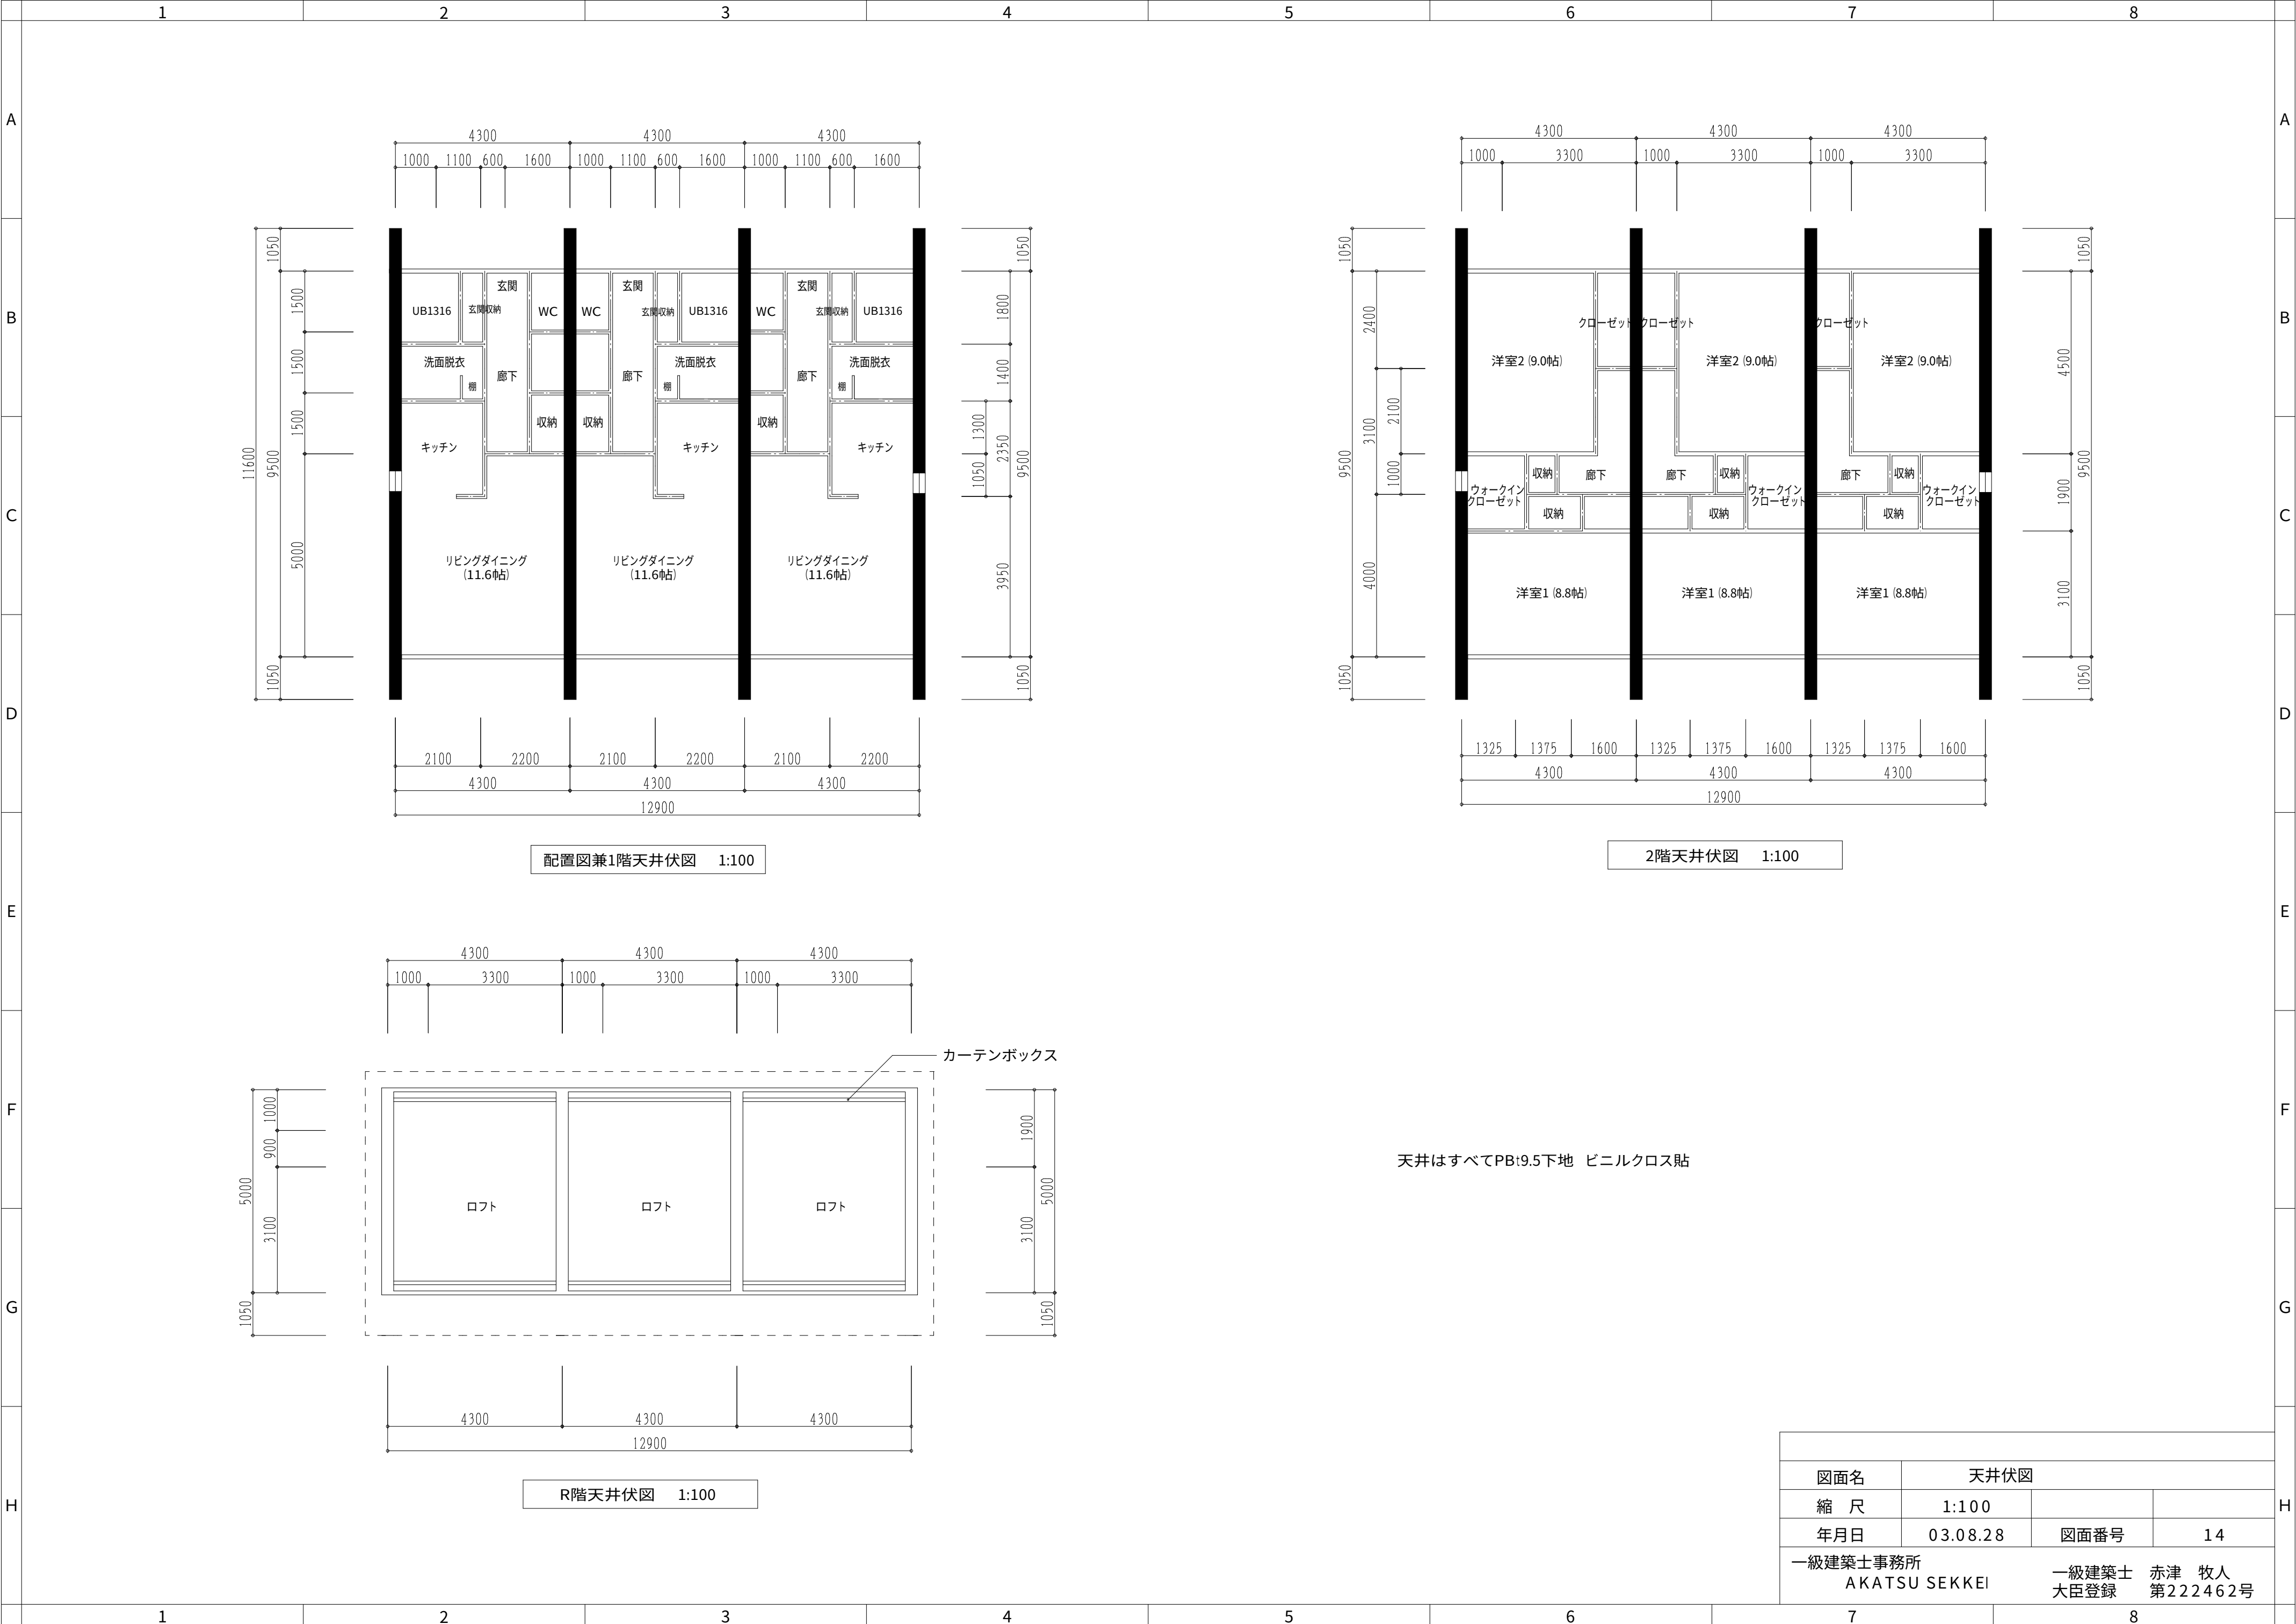

図面名			
天井伏図			
縮 尺	1:100		
年月日	03.08.28	図面番号	14
一級建築士事務所 AKATSU SEKKEI		一級建築士 大臣登録	赤津 牧人 第222462号

